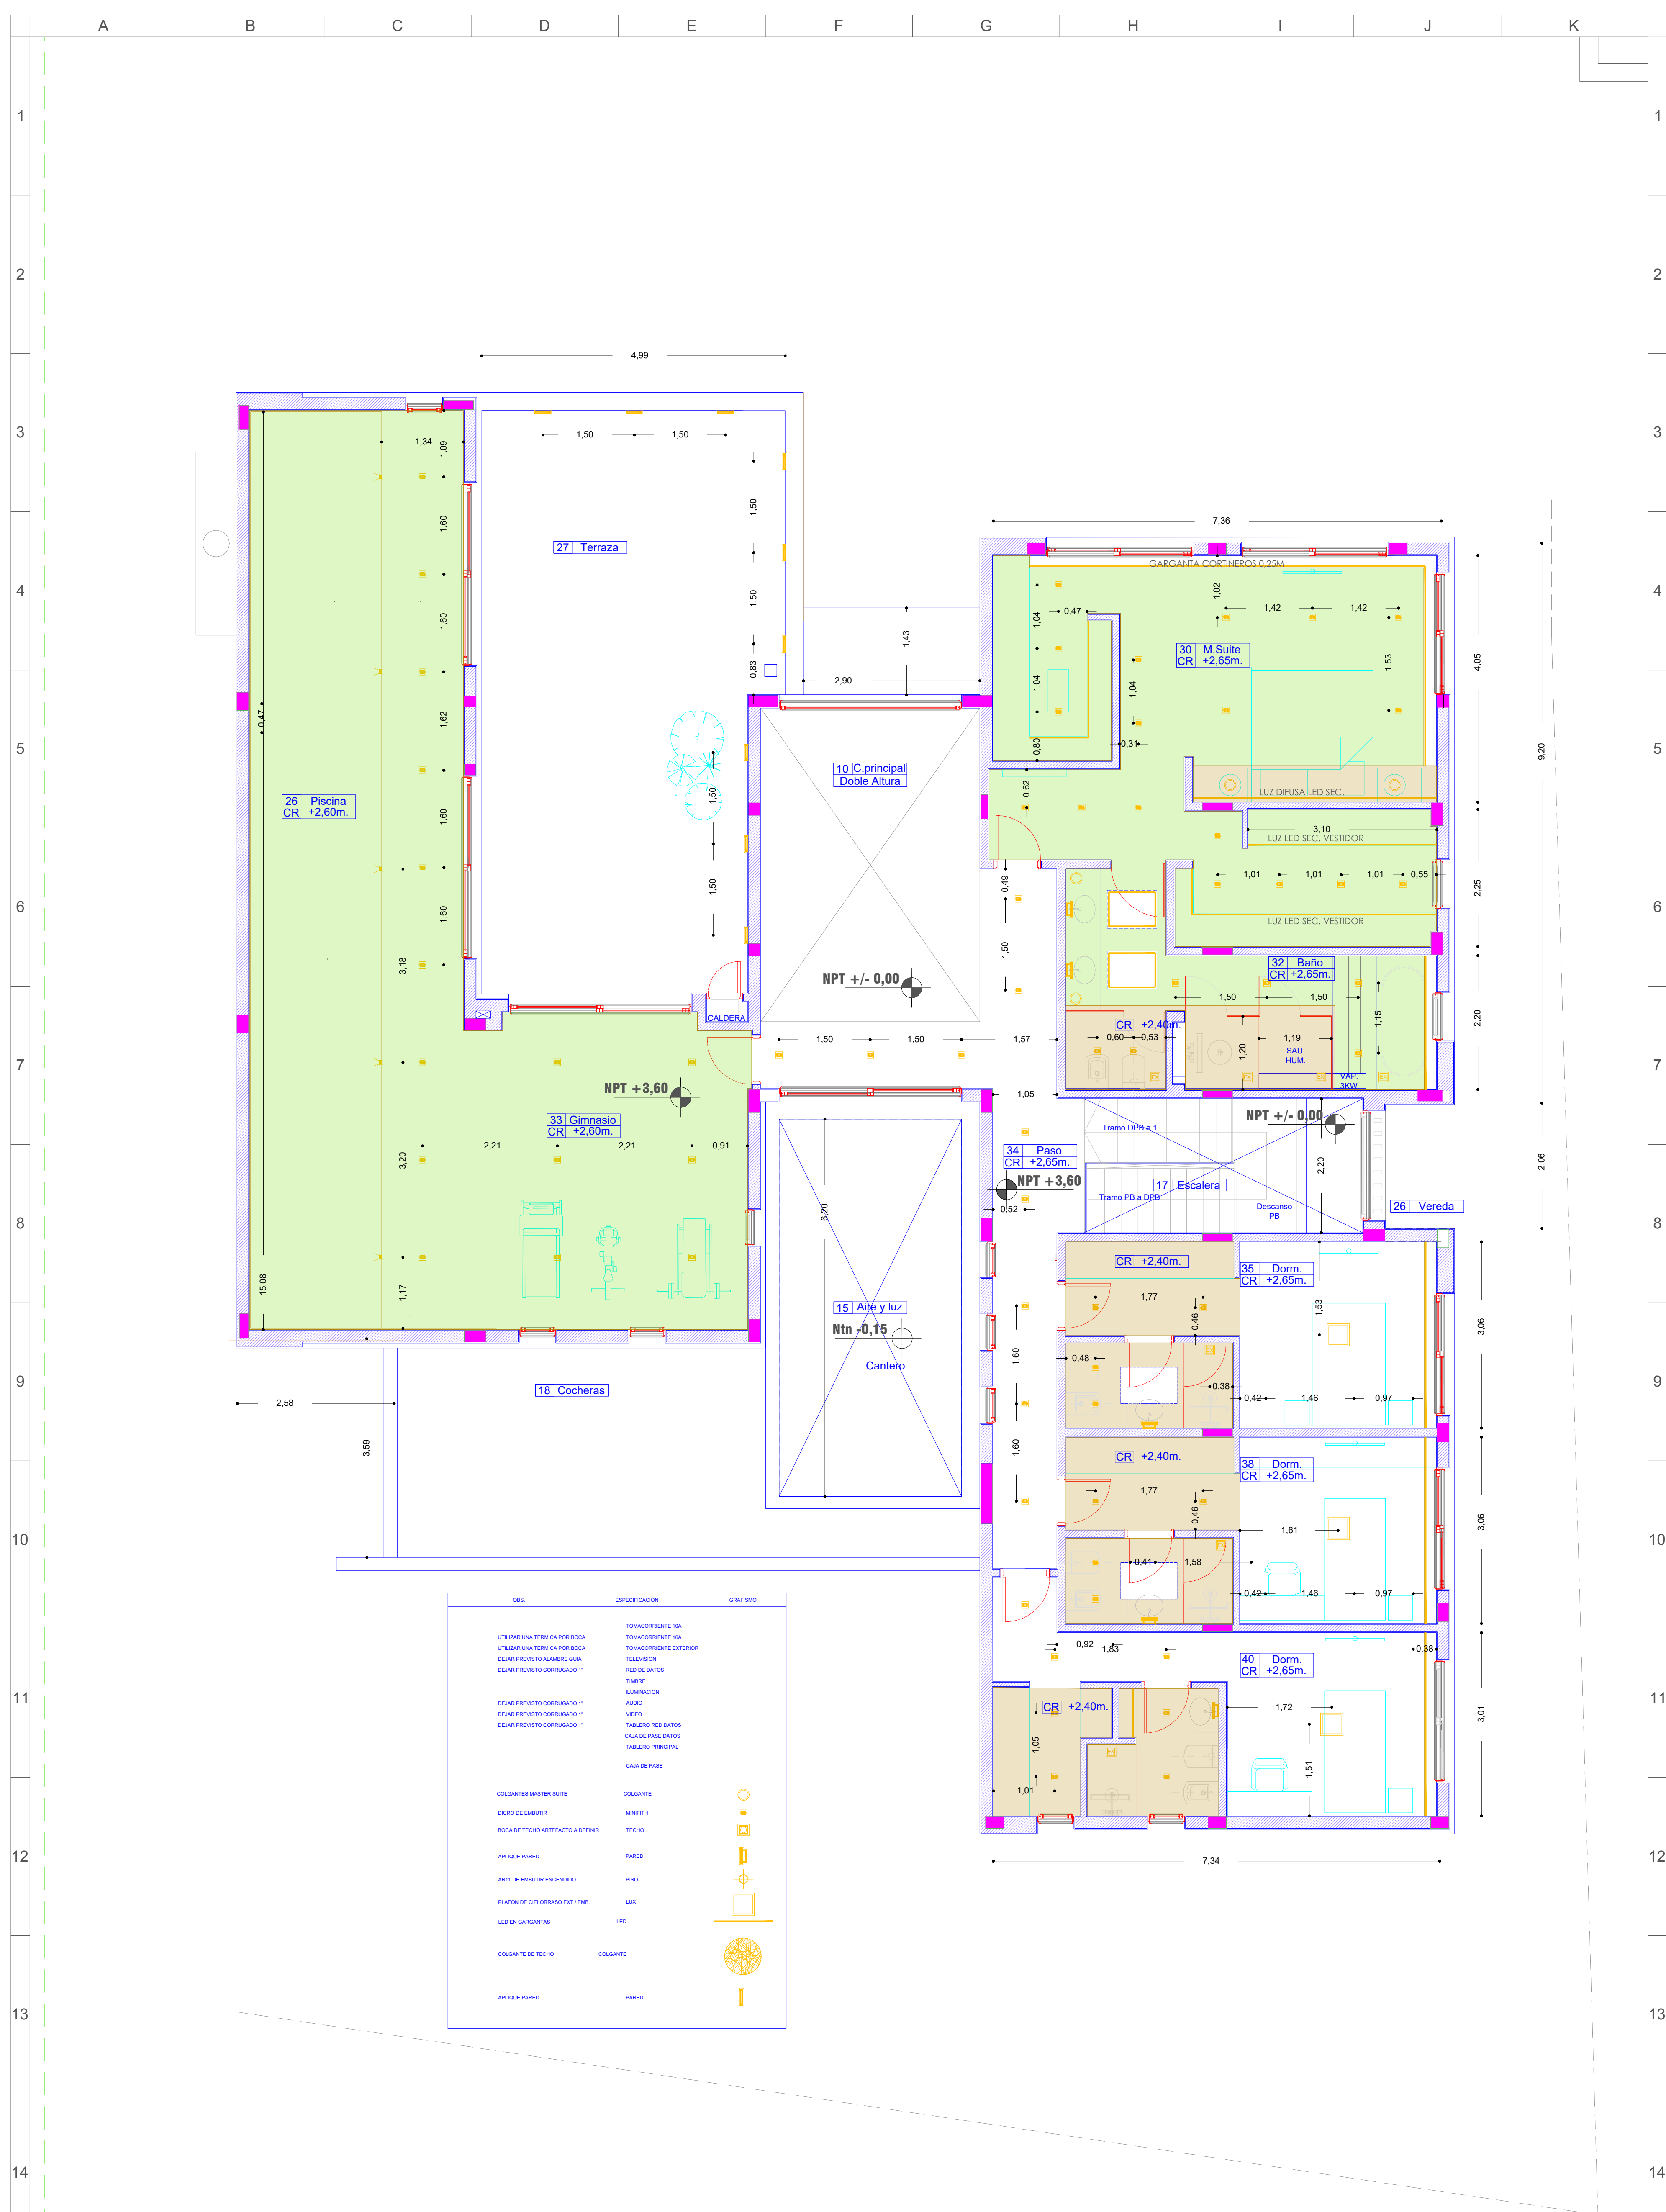


CIELORRASOS

DENOMINACION PLANO

OG 403 CR PA

CIELORRASOS PA

ESC : 1/50

NOTA:

- SE CONSIDERA 14CM DE DISTANCIA LA SEPARACION DE COMANDOS DE RETORNOS Y VANOS DE PUERTAS.
- TODAS LAS MEDIDAS SERAN VERIFICADAS EN OBRA POR EL CONTRATISTA.
- DESCRIPCION DE TIPOS DE CIELORRASOS SEGÚN PLANILLAS DE CIELORRASOS ADJUNTAS.
- VER DETALLES DE GARGANTAS
- VER DETALLES DE CORTINEROS
- VER DETALLE ENCUENTRO GOTERONES EN SEMICUBIERTOS

Vicente J. Fumagalli

Contacto: infovjf@gmail.com
+54 9 11 39991707

Obra: Vivienda unifamiliar
Dirección: Barrio Olivos Golf Club Lote 7
Ruta Panamericana km 32 Bs. As.

Revision : 10 26

Apto ejecución :

