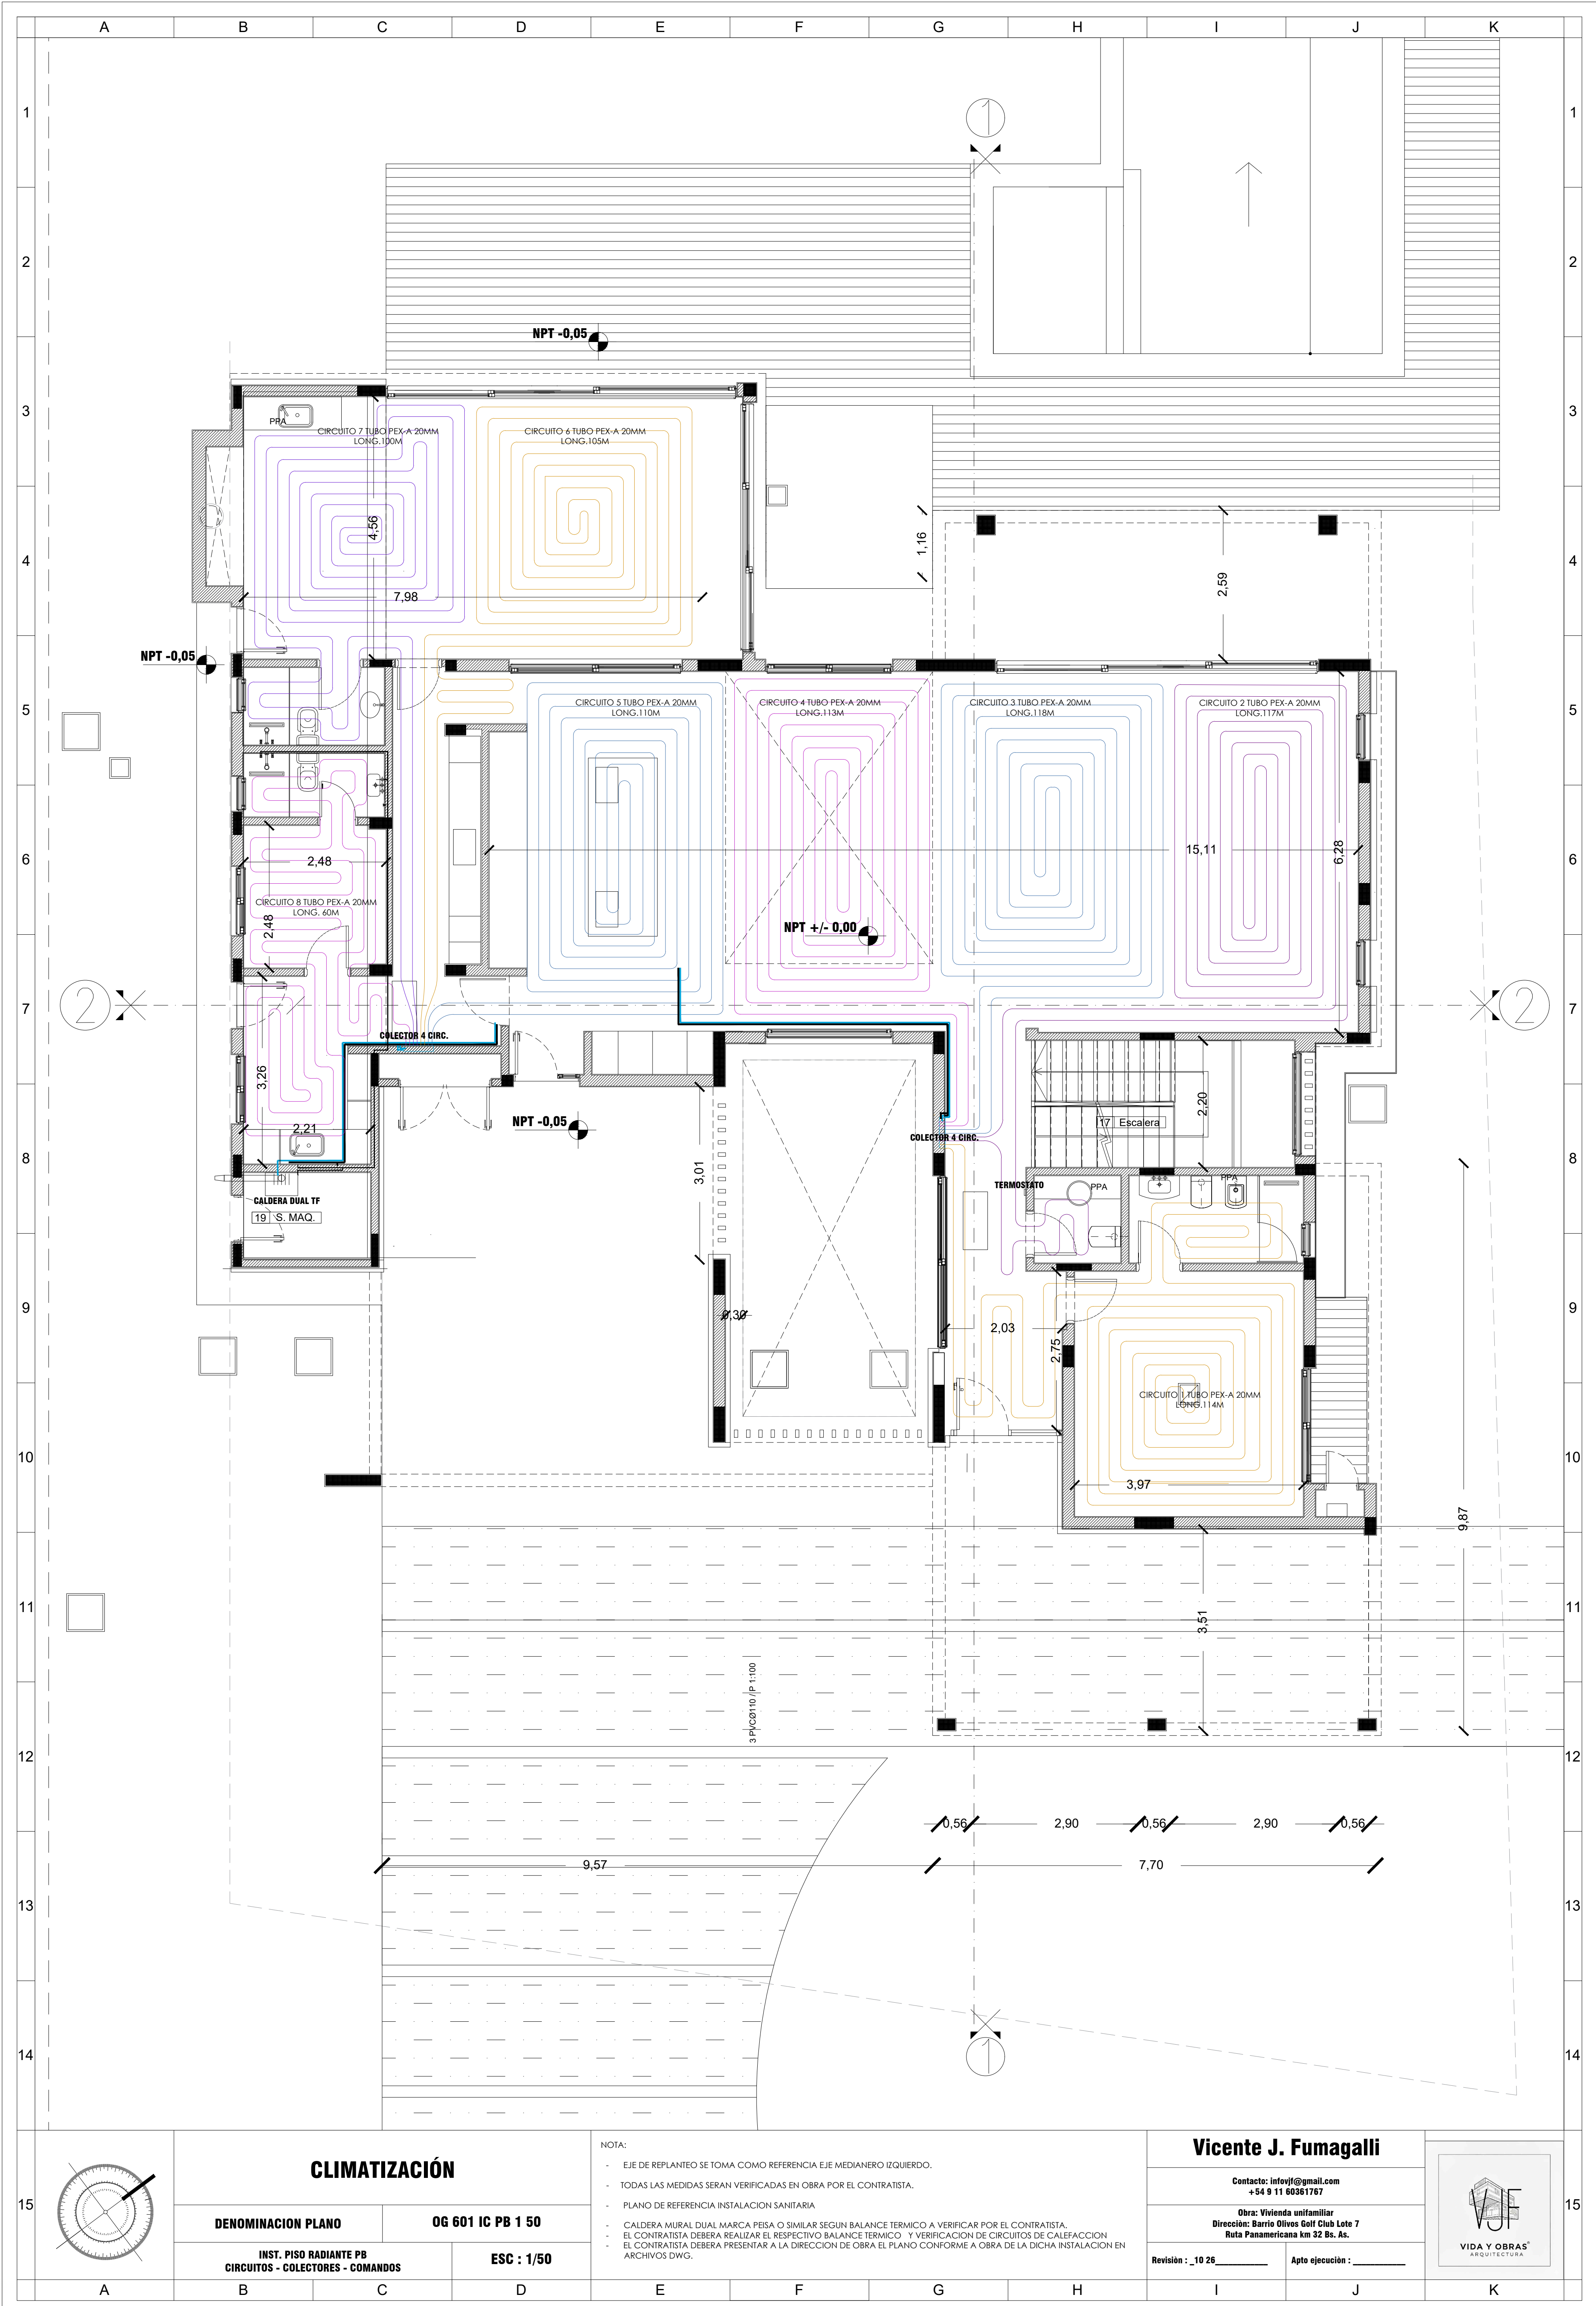


CLIMATIZACIÓN

DENOMINACION PLANO
OG 601 IC PB 1 50

INST. PISO RADIANTE PB
CIRCUITOS - COLECTORES - COMANDOS

ESC : 1/50

- NOTA:
- EJE DE REPLANTEO SE TOMA COMO REFERENCIA EJE MEDIANERO IZQUIERDO.
 - TODAS LAS MEDIDAS SERAN VERIFICADAS EN OBRA POR EL CONTRATISTA.
 - PLANO DE REFERENCIA INSTALACION SANITARIA
 - CALDERA MURAL DUAL MARCA PEISA O SIMILAR SEGUN BALANCE TERMICO A VERIFICAR POR EL CONTRATISTA.
 - EL CONTRATISTA DEBERA REALIZAR EL RESPECTIVO BALANCE TERMICO Y VERIFICACION DE CIRCUITOS DE CALEFACCION
 - EL CONTRATISTA DEBERA PRESENTAR A LA DIRECCION DE OBRA EL PLANO CONFORME A OBRA DE LA DICHA INSTALACION EN ARCHIVOS DWG.

Vicente J. Fumagalli

Contacto: infovjf@gmail.com
+54 9 11 60361767

Obra: Vivienda unifamiliar
Direccion: Barrio Olivos Golf Club Lote 7
Ruta Panamericana km 32 Bs. As.

Revisión : 10 26 Apto ejecución : _____

