


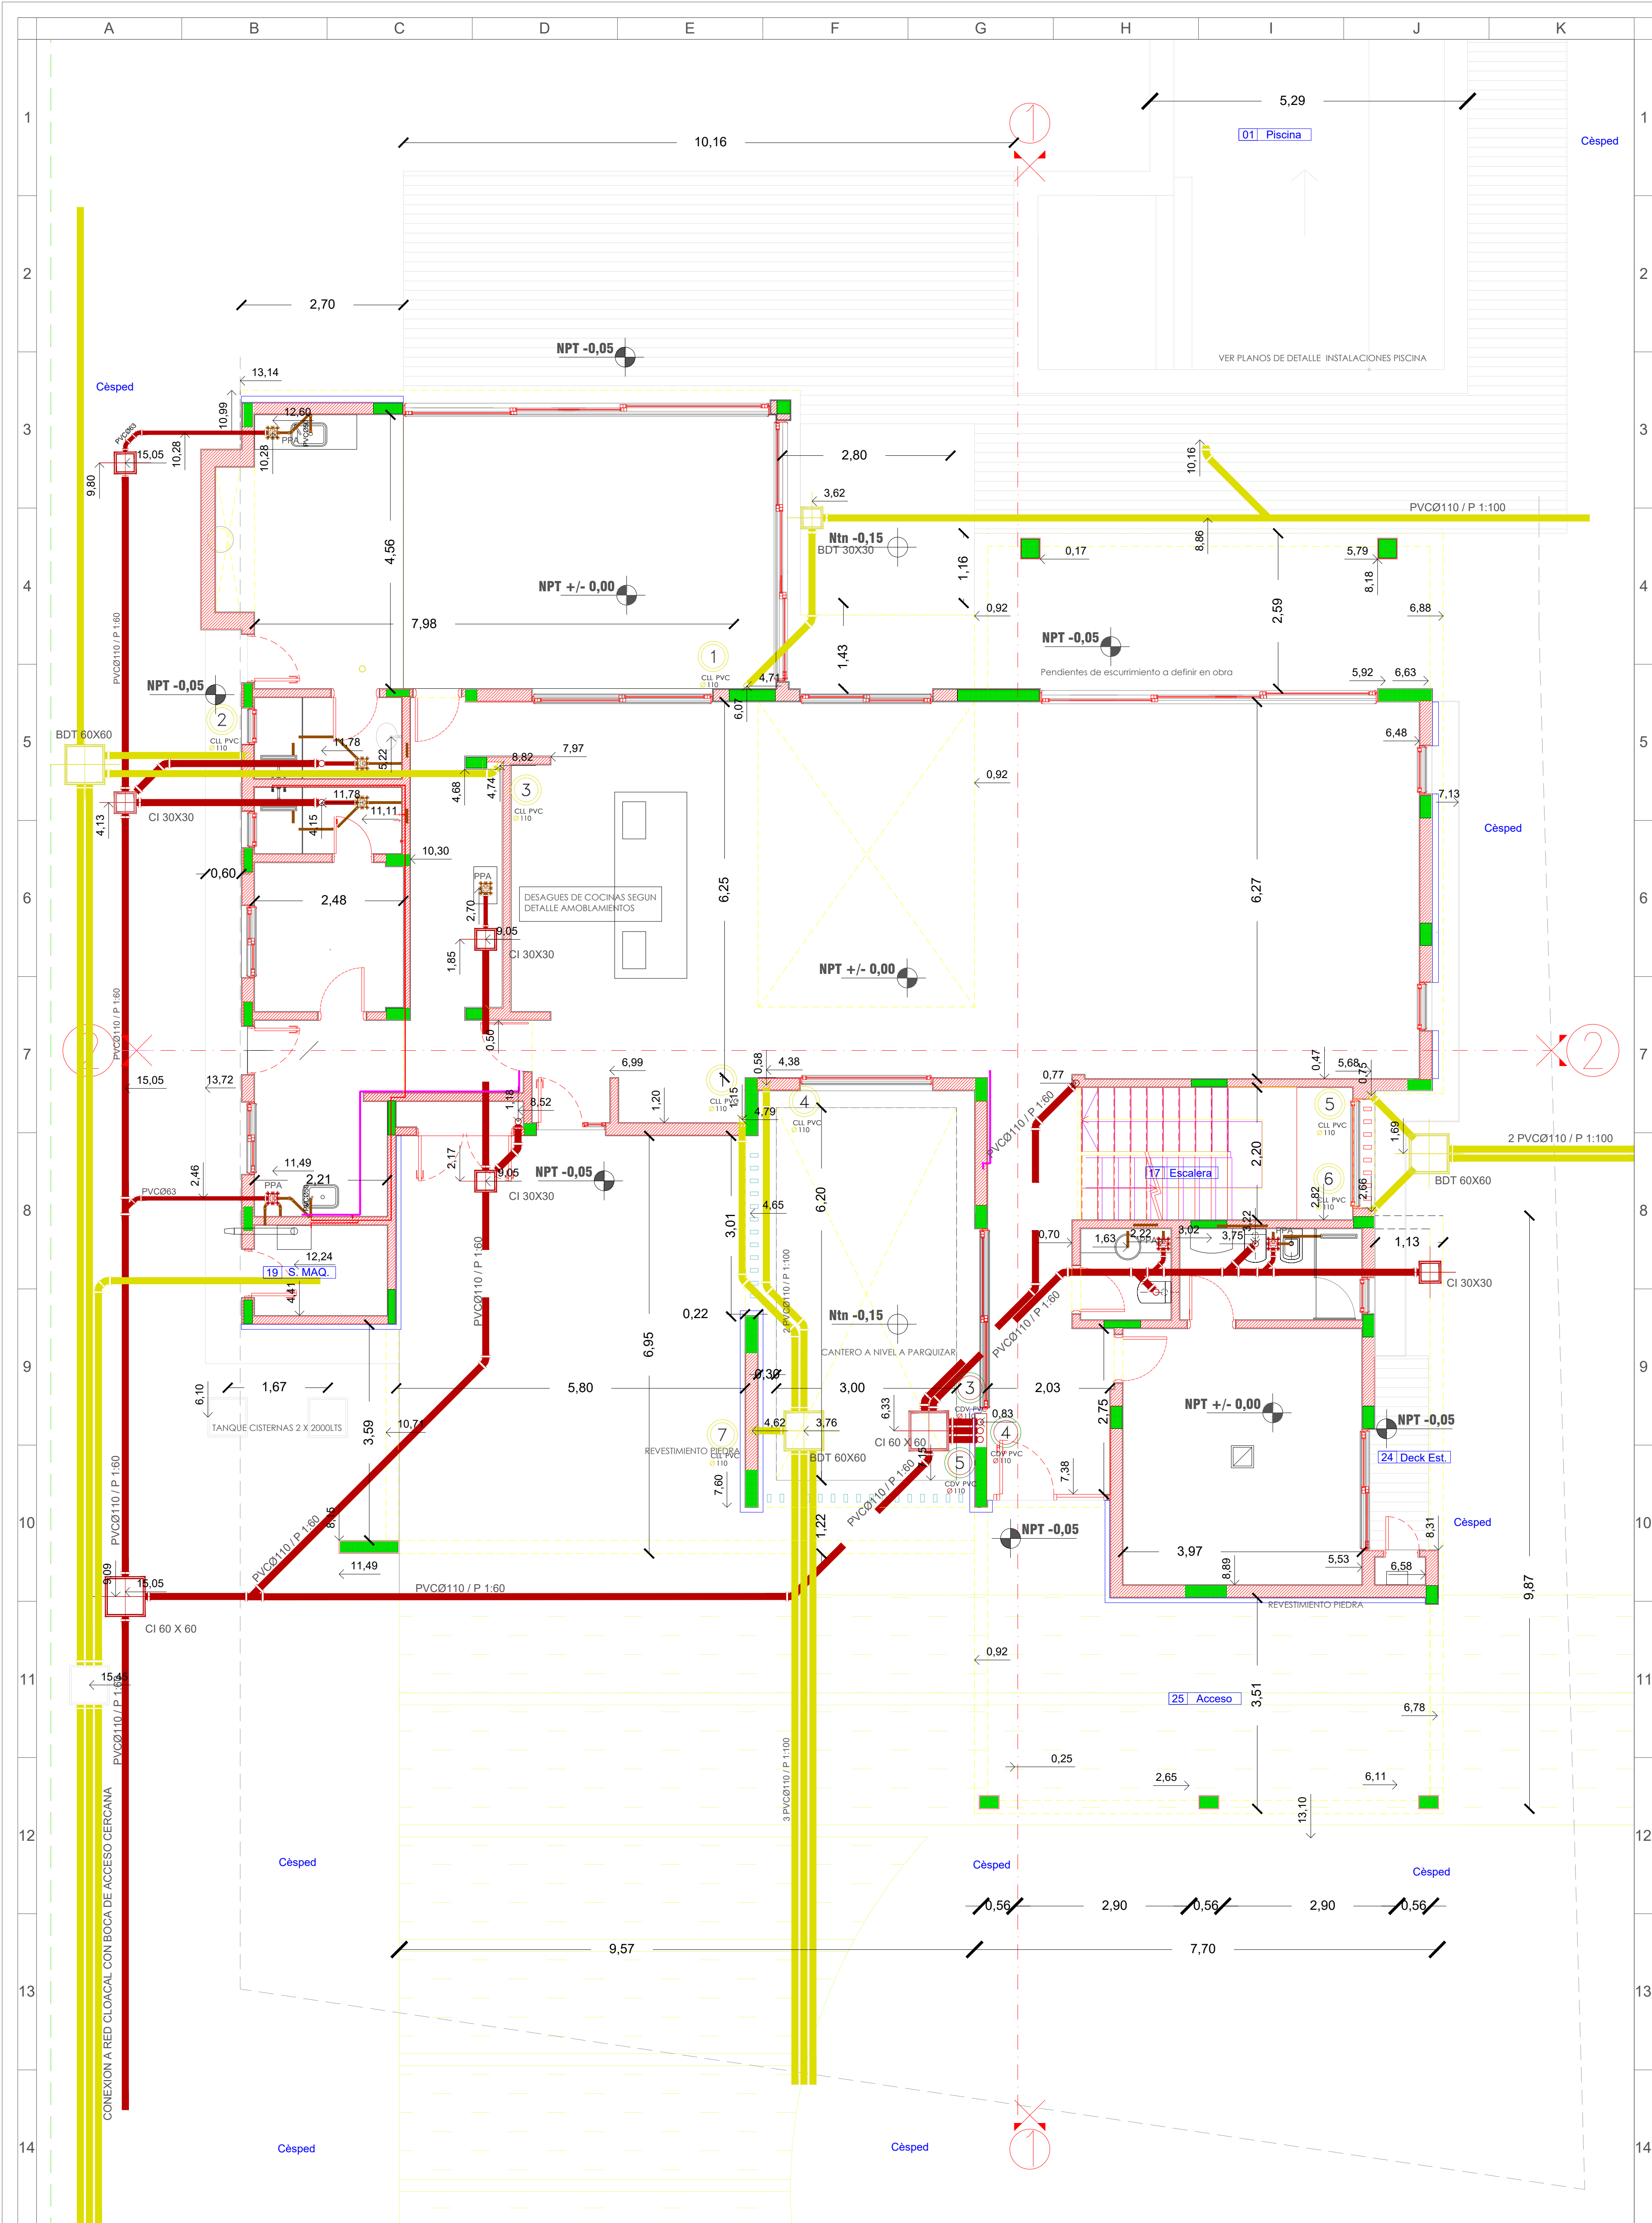

	INSTALACION SANITARIA		NOTA: - EJE DE REPLANTEO SE TOMA COMO REFERENCIA EJE MEDIANERO IZQUIERDO. - TODAS LAS MEDIDAS SERAN VERIFICADAS EN OBRA POR EL CONTRATISTA. - PLANO DE REFERENCIA INSTALACION SANITARIA - EN SOLADOS CON INCLINACION SEMICUBIERTOS Y EXTERIORES, SE INDICA NIVEL MAS ALTO. POR LO QUE DEBEN TENERSE EN CUENTA PENDIENTES DE ESCURRIMIENTO DE AGUA. ESTE PLANO NO CONTEMPLA ESPESOR DE REVESTIMIENTOS DE MUROS SE VALIDARA CADA CASO CON PLANOS DE DETALLE	Vicente J. Fumagalli						
	DENOMINACION PLANO			Contacto: infovj@gmail.com +54 9 11 60361767						
	INST. DESAGUES PLUVIALES / CLOCALES PB			Obra: Vivienda unifamiliar Direccion: Barrio Olivos Golf Club Lote 7 Ruta Panamericana km 32 Bs. As.						
A	B	C	D	E	F	G	H	I	J	K