
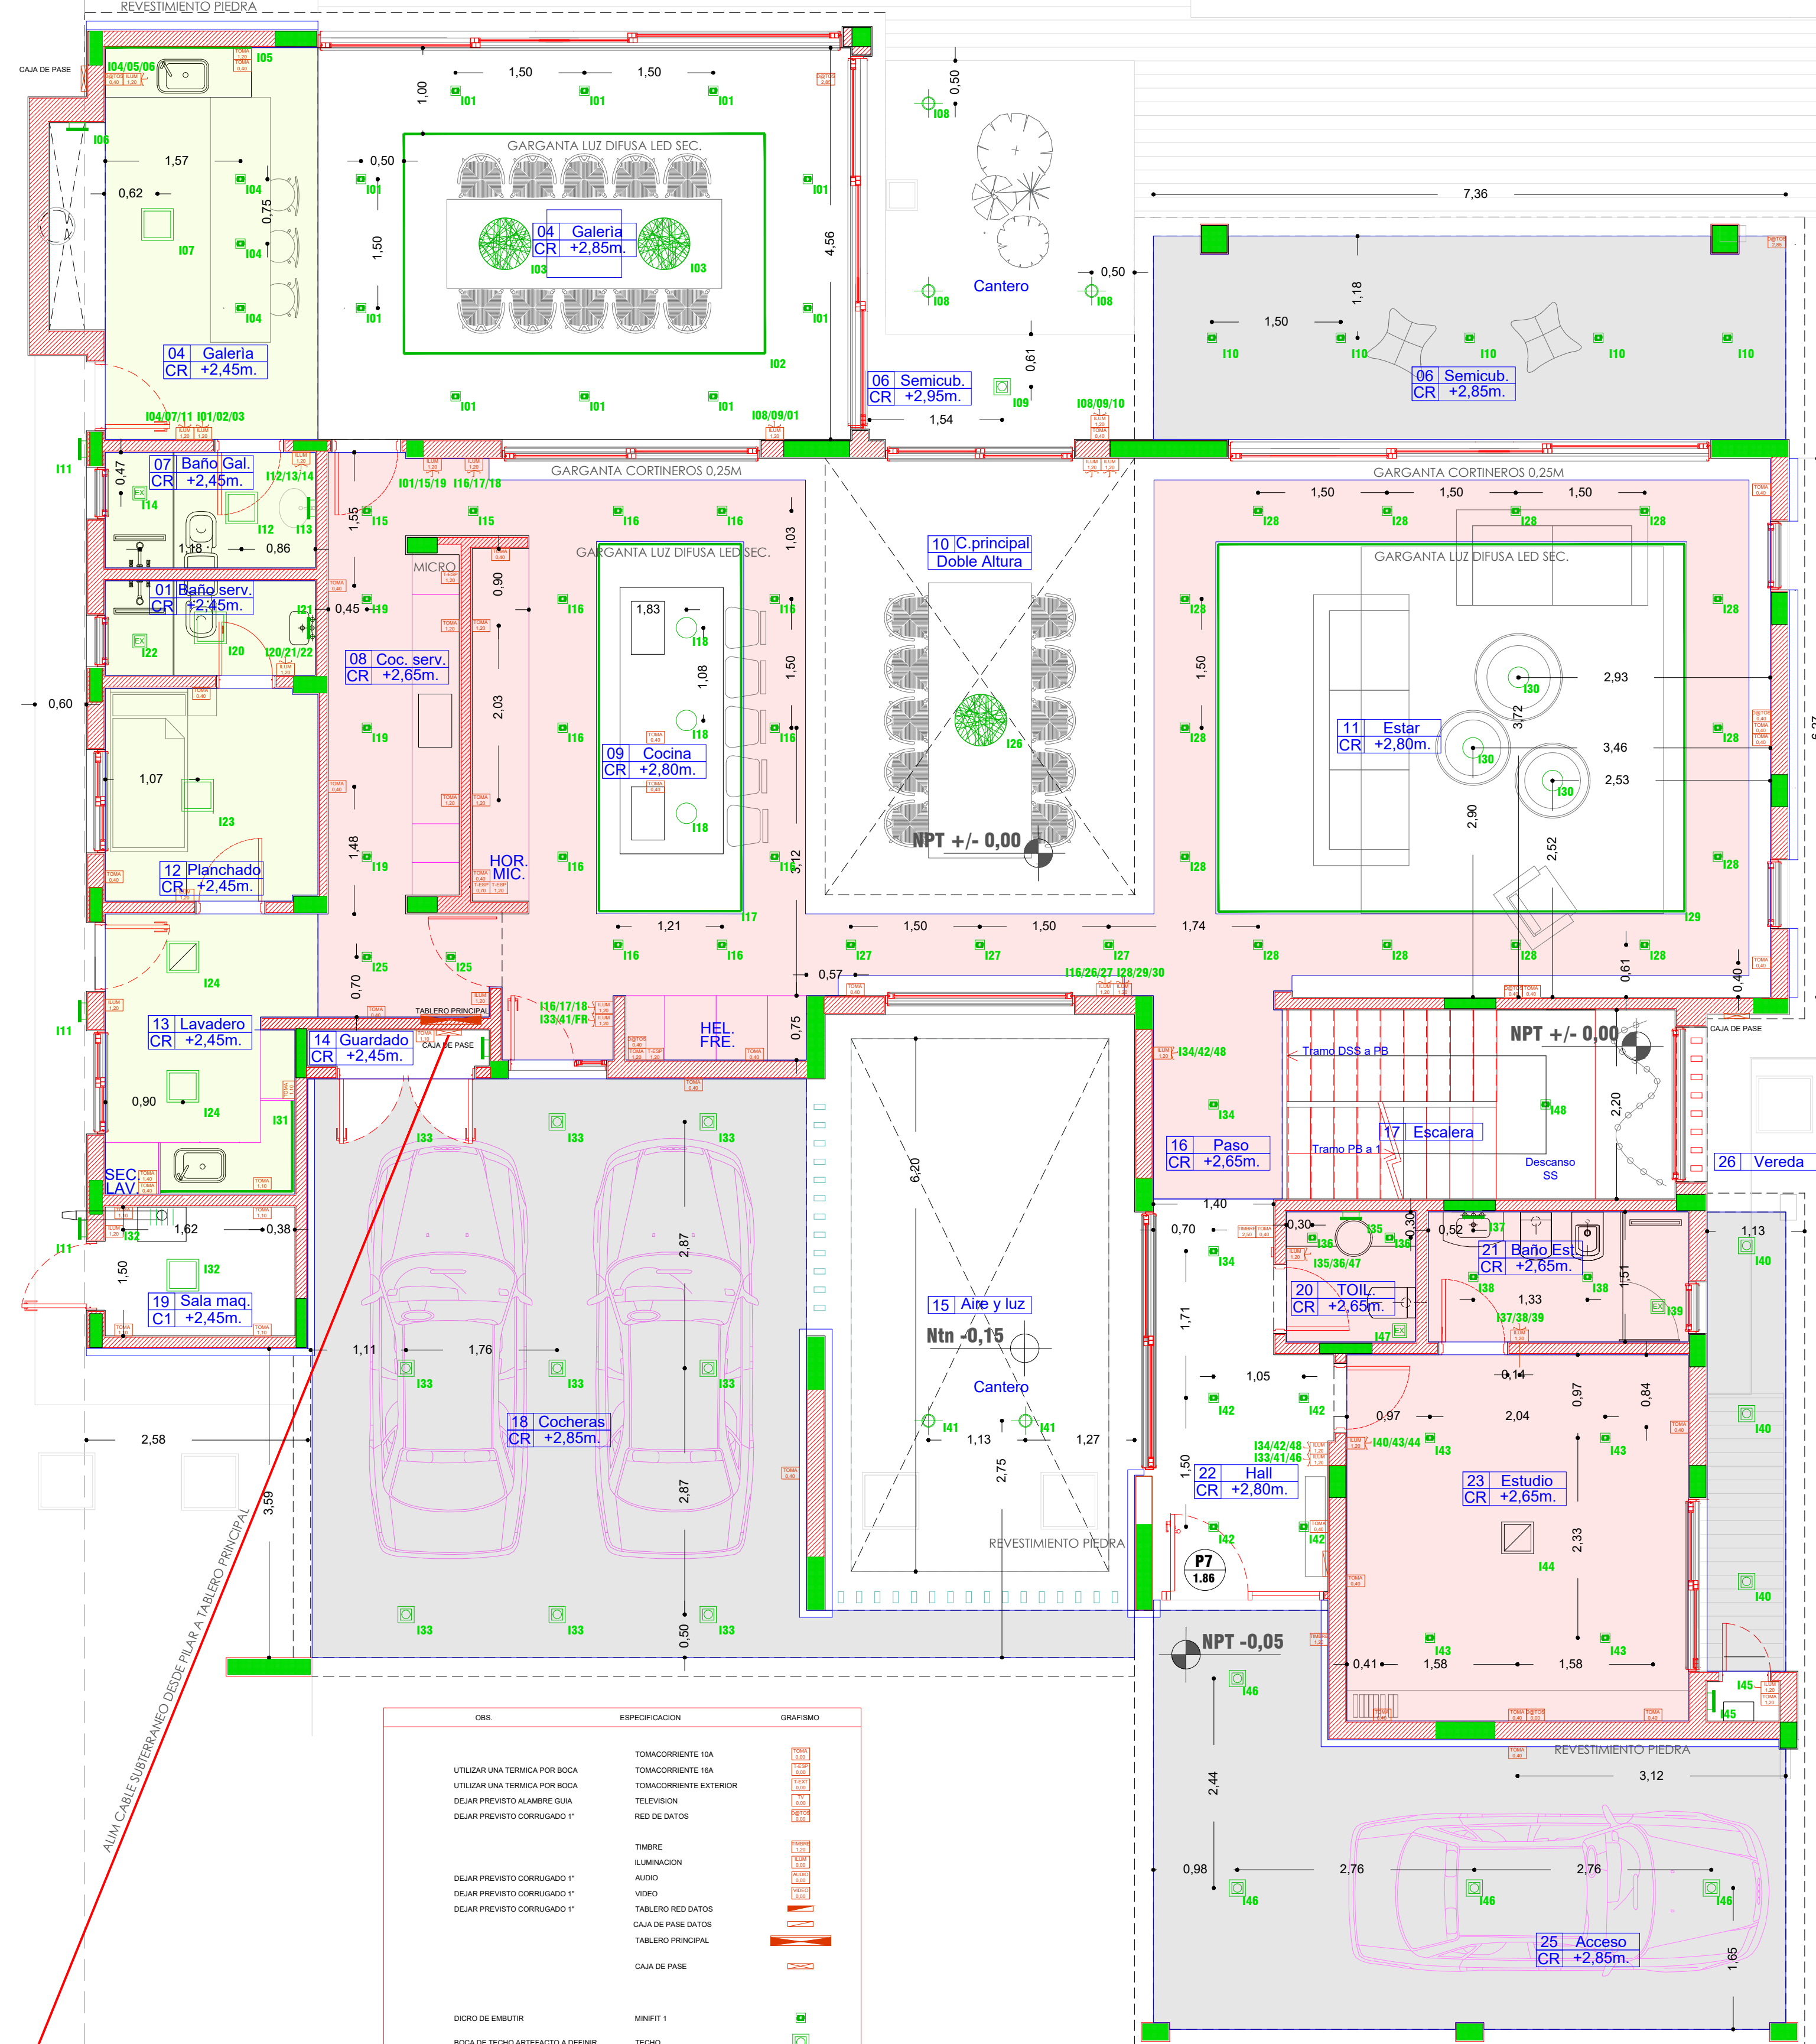


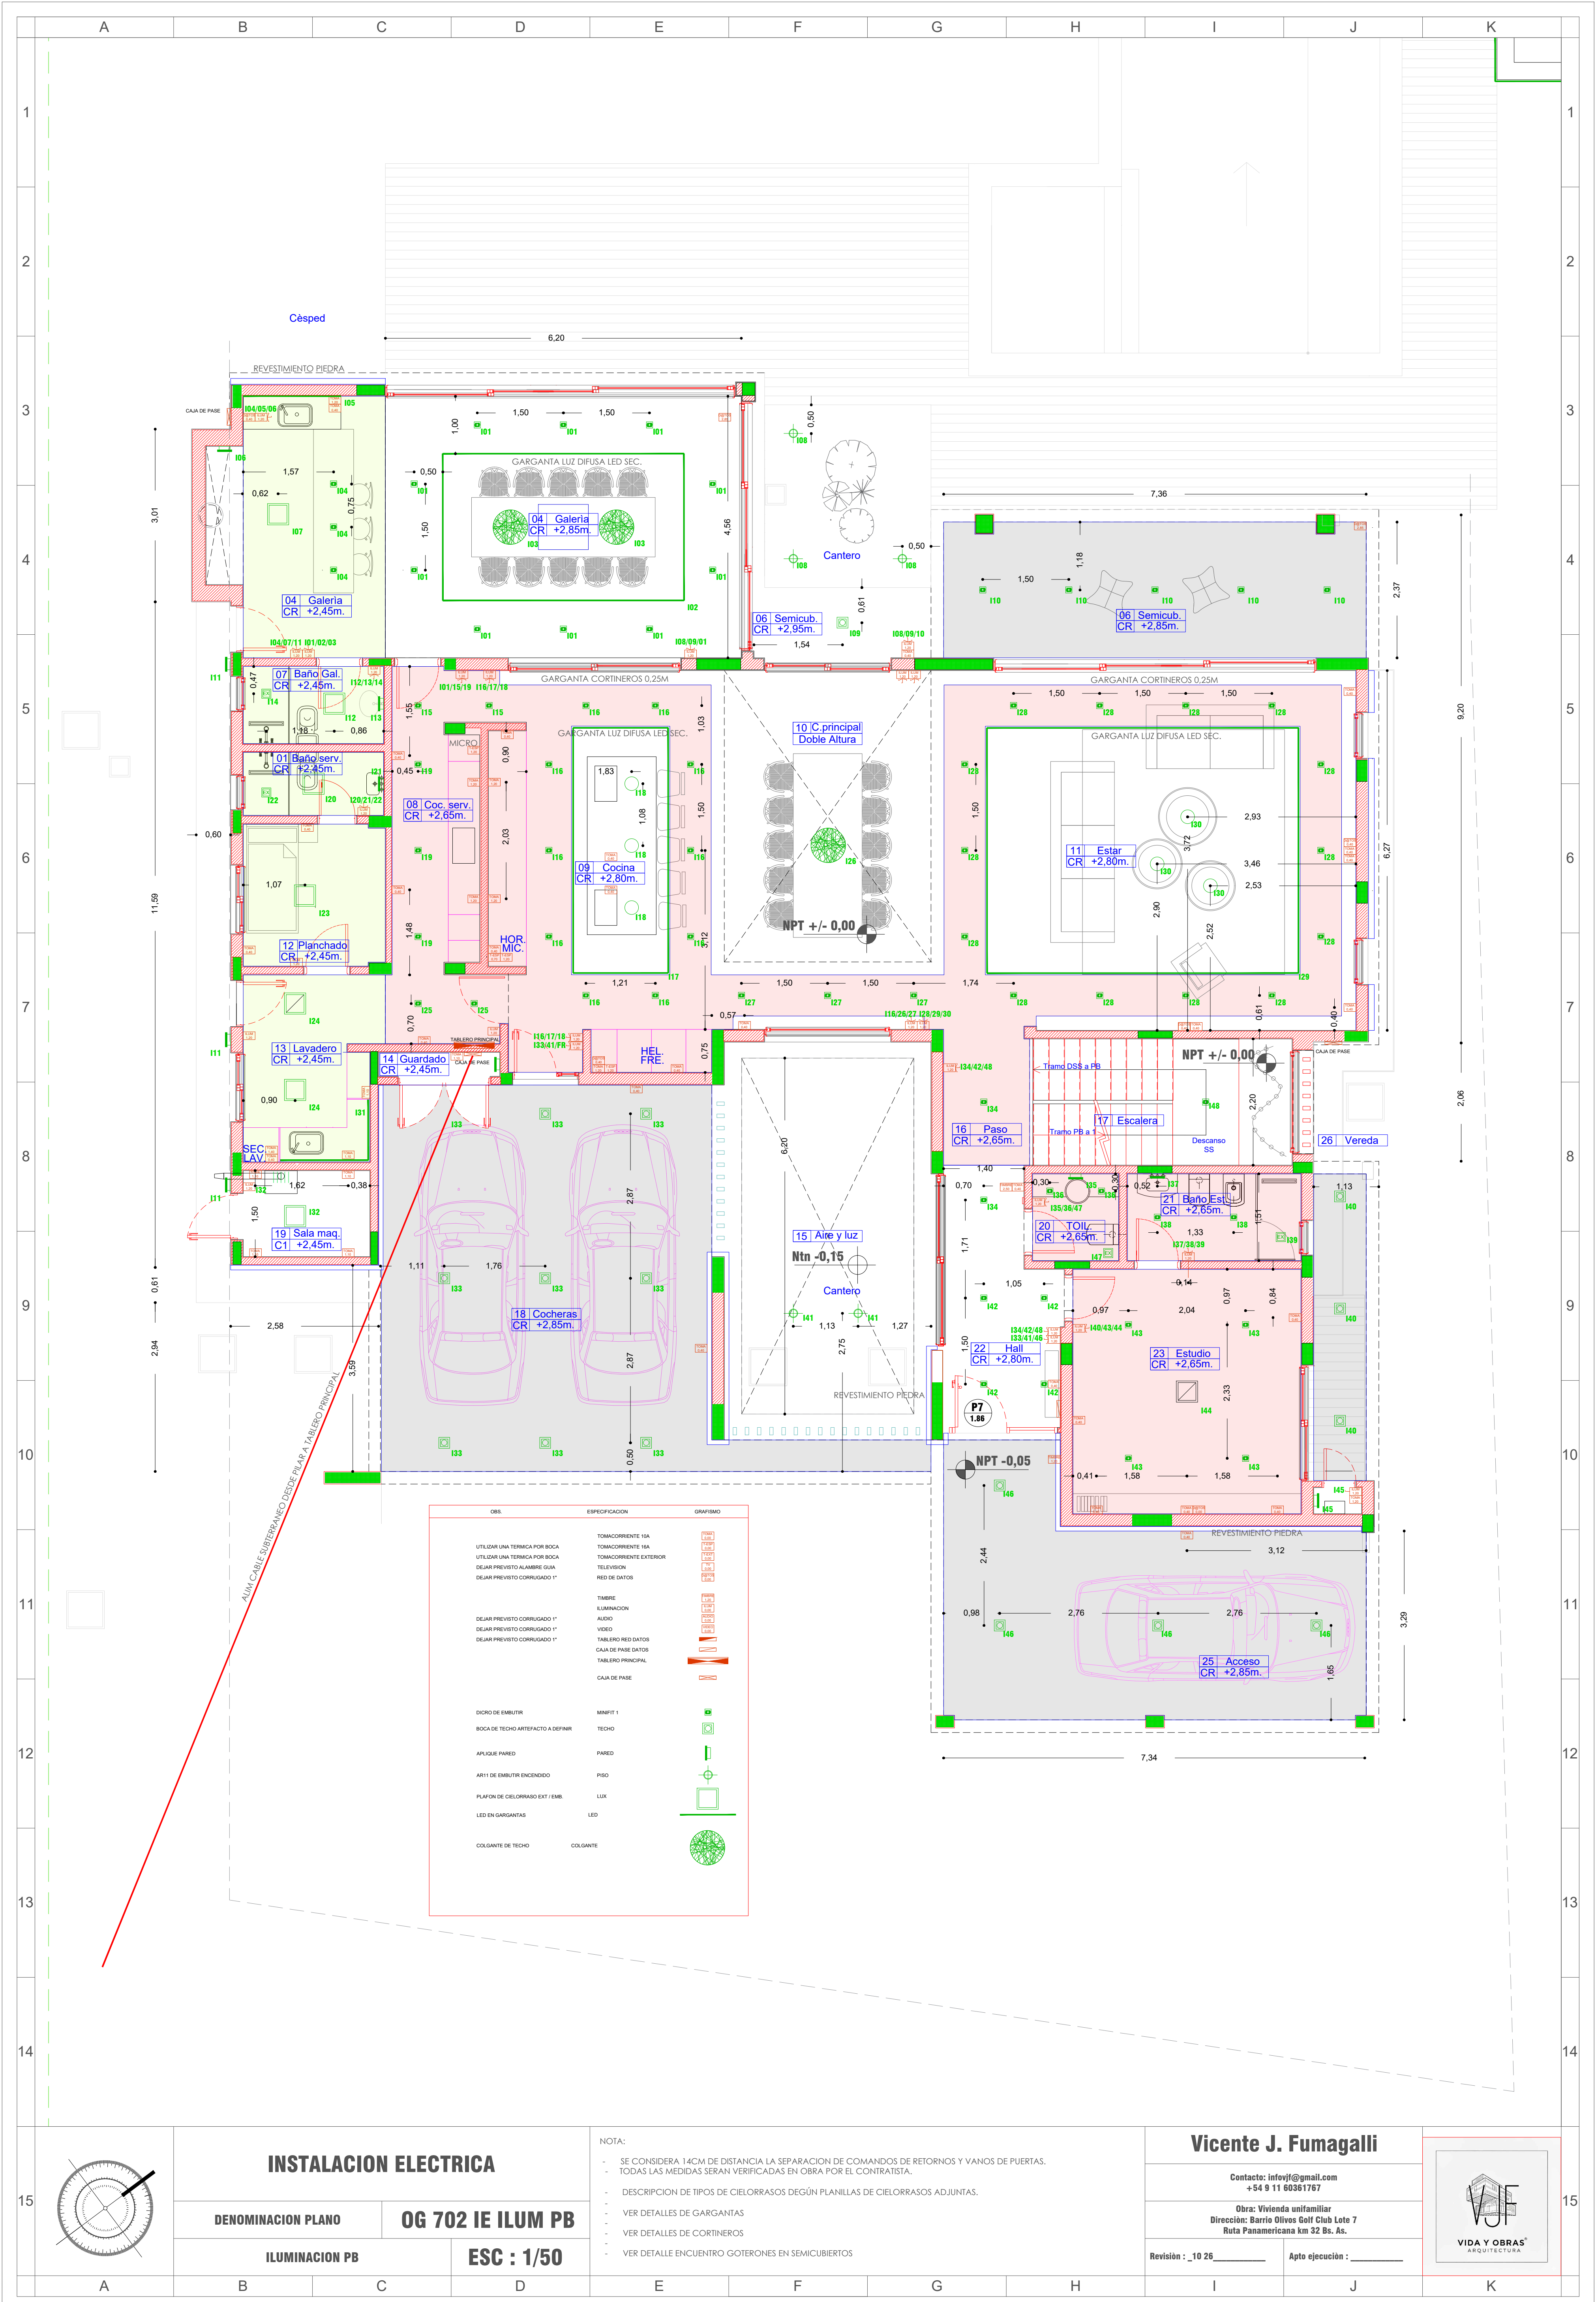

ORIS	ESPECIFICACION	GRAFISMO
UTILIZAR UNA TECNICA POR BOCA	TOMACORRIENTE 10A	
UTILIZAR UNA TECNICA POR BOCA	TOMACORRIENTE 15A	
DEJAR PREVISTO ALAMBRE GUIA	TOMACORRIENTE EXTERIOR	
DEJAR PREVISTO CORRUGADO 1"	TELEVISION	
	RED DE DATOS	
DEJAR PREVISTO CORRUGADO 1"	TIMBRE	
DEJAR PREVISTO CORRUGADO 1"	ILUMINACION	
DEJAR PREVISTO CORRUGADO 1"	AUDIO	
DEJAR PREVISTO CORRUGADO 1"	VIDEO	
	TABLERO RED DATOS	
	CAJA DE PASE DATOS	
	TABLERO PRINCIPAL	
	CAJA DE PASE	
DICRO DE EMBUTIR	MANFIT 1	
BOCA DE TECHO ARTEFACTO A DEFINIR	TECHO	
APUQUE PARED	PARED	
ART1 DE EMBUTIR ENCENDIDO	PISO	
PLAFON DE CIELORRASOS EXT/EMB	LUX	
LED EN GARGANTAS	LED	
COLGANTE DE TECHO	COLGANTE	

- NOTA:
- SE CONSIDERA 14CM DE DISTANCIA LA SEPARACION DE COMANDOS DE RETORNOS Y VANOS DE PUERTAS.
 - TODAS LAS MEDIDAS SERAN VERIFICADAS EN OBRA POR EL CONTRATISTA.
 - DESCRIPCION DE TIPOS DE CIELORRASOS SEGUN PLANILLAS DE CIELORRASOS ADJUNTAS.
 - VER DETALLES DE GARGANTAS
 - VER DETALLES DE CORTINEROS
 - VER DETALLE ENCUENTRO GOTERONES EN SEMICUBIERTOS

Vicente J. Fumagalli

Contacto: infovjf@gmail.com
+54 9 11 60361767

Obra: Vivienda unifamiliar
Direccion: Barrio Olivos Golf Club Lote 7
Ruta Panamericana km 32 Bs. As.

Revisión : _10 26_ Apto ejecución : _____

