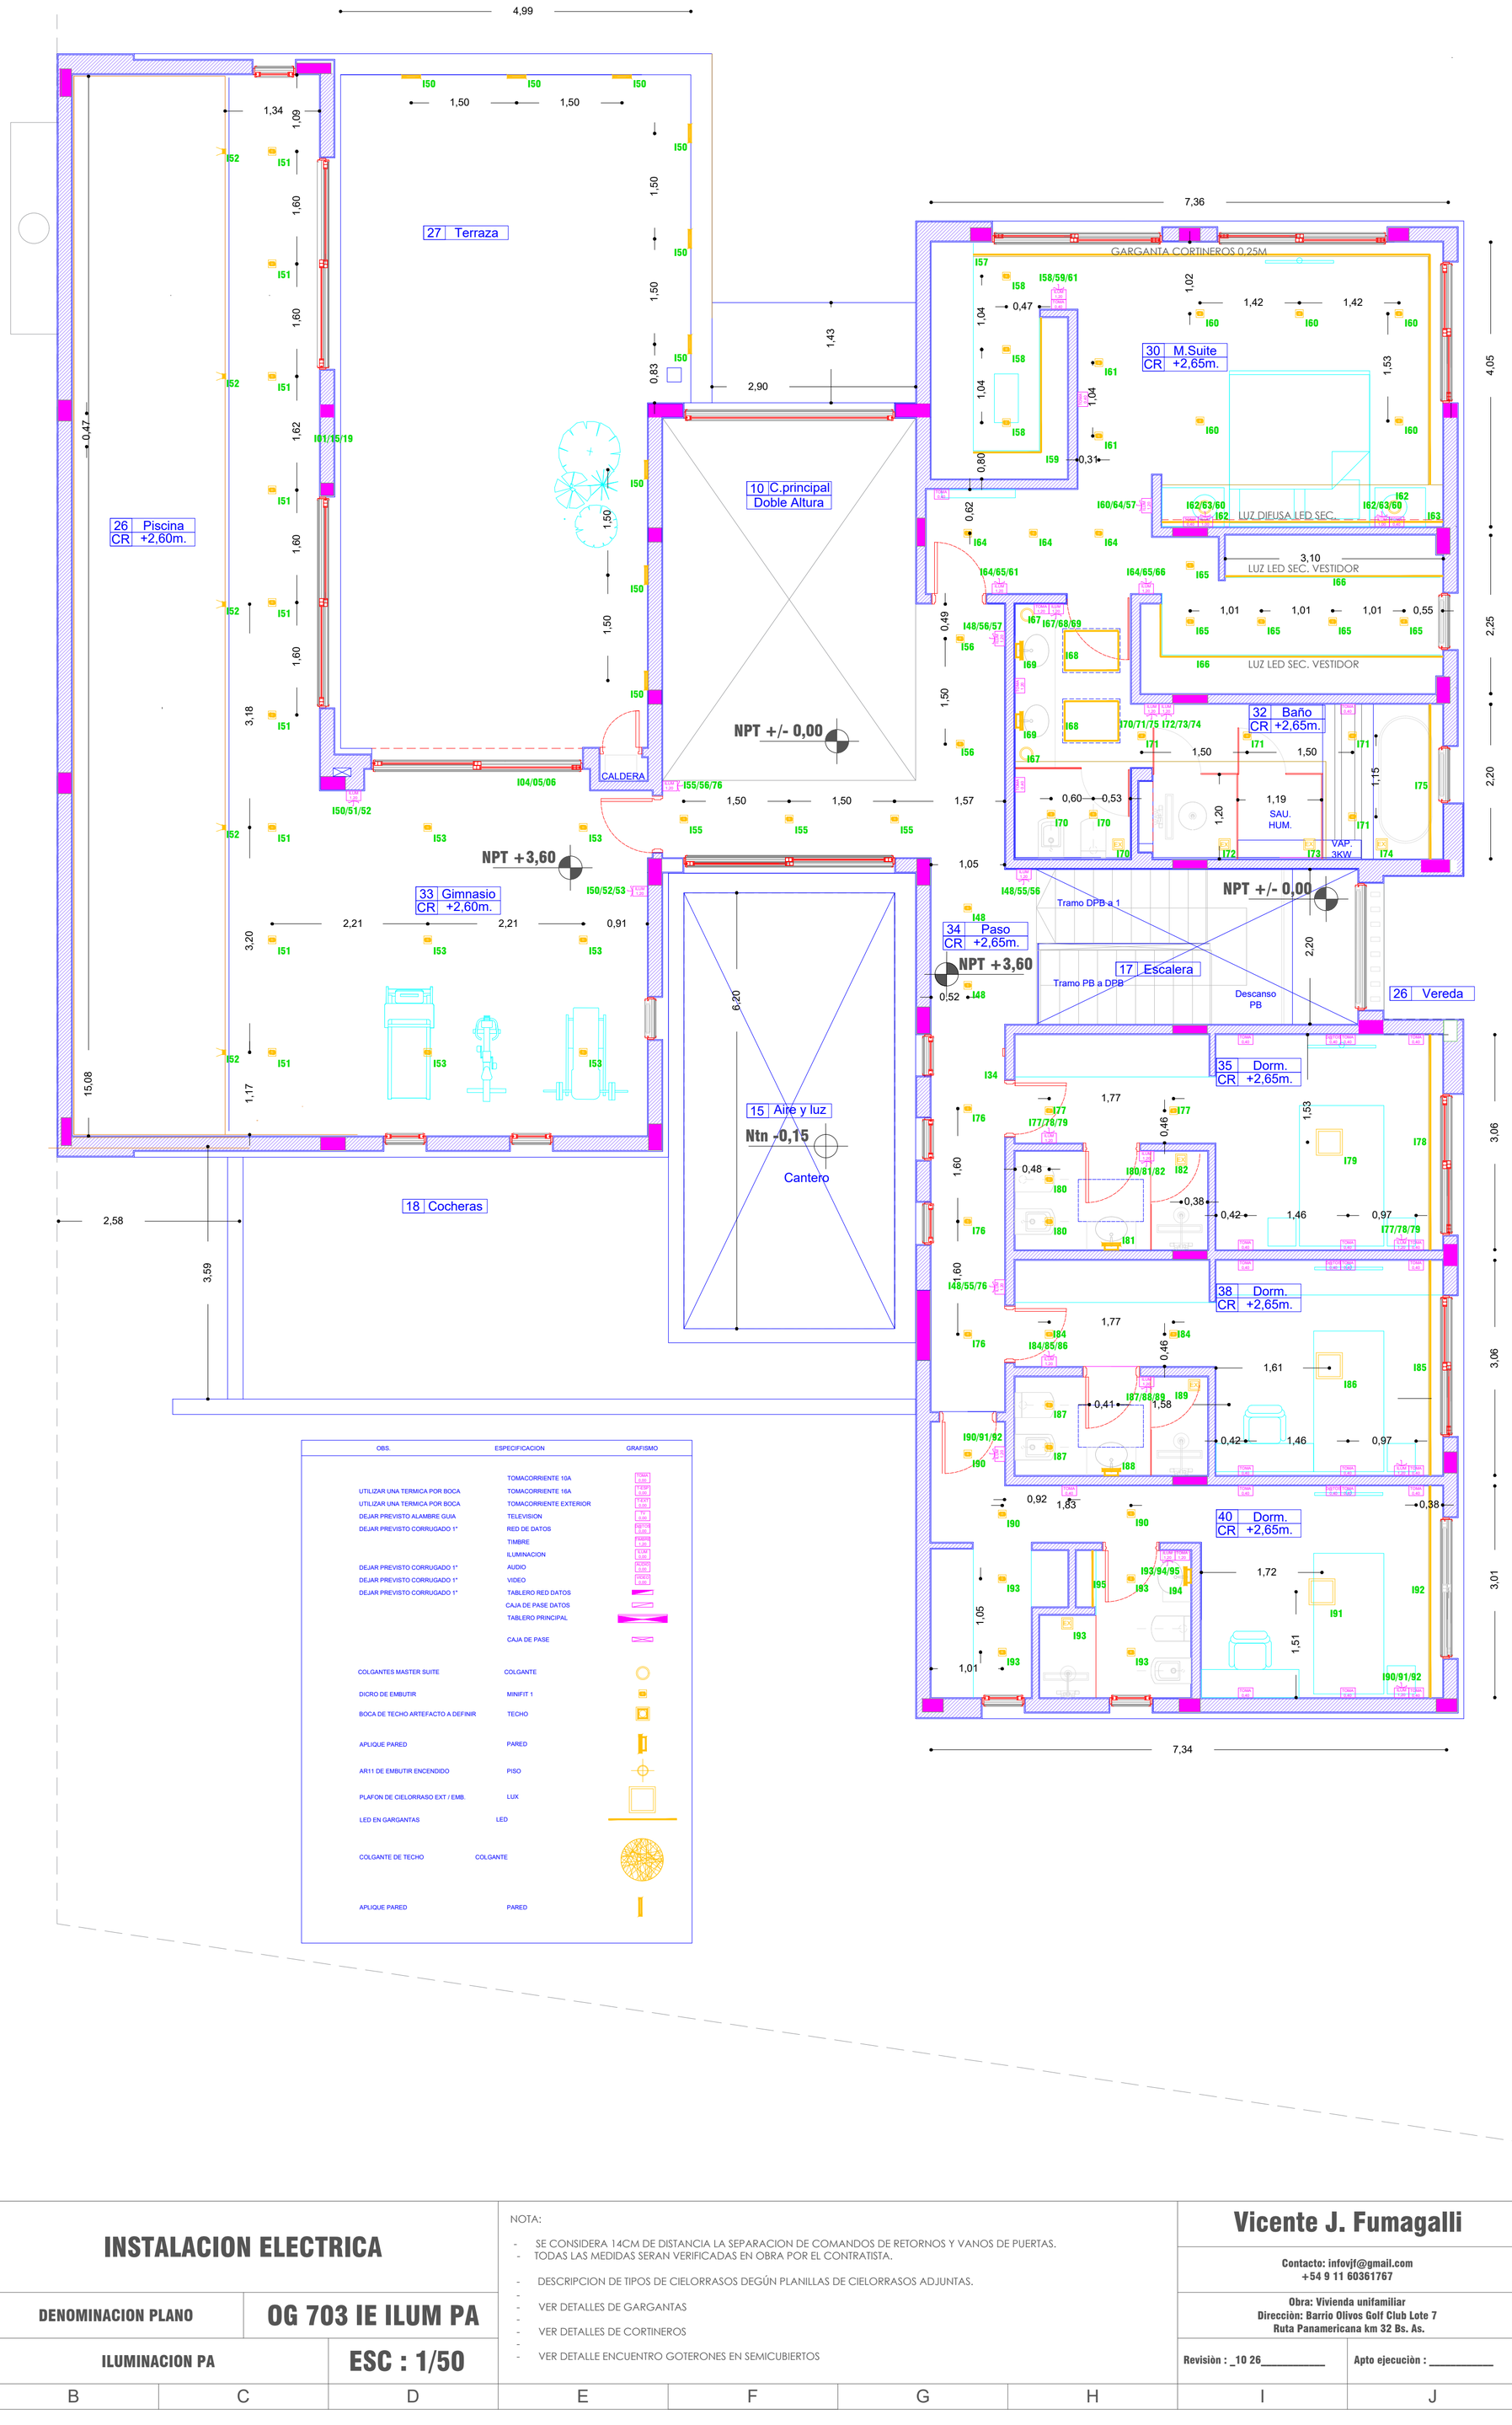

OBS.	ESPECIFICACION	GRAFISMO
	TOMACORRIENTE 10A	
UTILIZAR UNA TERMICA POR BOCA	TOMACORRIENTE 16A	
UTILIZAR UNA TERMICA POR BOCA	TOMACORRIENTE EXTERIOR	
DEJAR PREVISTO ALAMBRE GUIA	TELEVISION	
DEJAR PREVISTO CORRUGADO 1"	RED DE DATOS	
	TIMBRE	
	ILUMINACION	
DEJAR PREVISTO CORRUGADO 1"	AUDIO	
DEJAR PREVISTO CORRUGADO 1"	VIDEO	
DEJAR PREVISTO CORRUGADO 1"	TABLERO RED DATOS	
	CAJA DE PASE DATOS	
	TABLERO PRINCIPAL	
	CAJA DE PASE	
COLGANTES MASTER SUITE	COLGANTE	
DICRO DE EMBUTIR	MINIFIT 1	
BOCA DE TECHO ARTEFACTO A DEFINIR	TECHO	
APLIQUE PARED	PARED	
AR11 DE EMBUTIR ENCENDIDO	PISO	
PLAFON DE CIELORRASO EXT / EMB.	LUX	
LED EN GARGANTAS	LED	
COLGANTE DE TECHO	COLGANTE	
APLIQUE PARED	PARED	

INSTALACION ELECTRICA

DENOMINACION PLANO	OG 703 IE ILUM PA
ILUMINACION PA	ESC : 1/50

NOTA:

- SE CONSIDERA 14CM DE DISTANCIA LA SEPARACION DE COMANDOS DE RETORNOS Y VANOS DE PUERTAS.
- TODAS LAS MEDIDAS SERAN VERIFICADAS EN OBRA POR EL CONTRATISTA.
- DESCRIPCION DE TIPOS DE CIELORRASOS DEGÚN PLANILLAS DE CIELORRASOS ADJUNTAS.
- VER DETALLES DE GARGANTAS
- VER DETALLES DE CORTINEROS
- VER DETALLE ENCUENTRO GOTERONES EN SEMICUBIERTOS

Vicente J. Fumagalli

Contacto: infovjf@gmail.com
+54 9 11 60361767

Obra: Vivienda unifamiliar
Direcciòn: Barrio Olivos Golf Club Lote 7
Ruta Panamericana km 32 Bs. As.

Revisiòn : _10 26_____ Apto ejecuciòn : _____

VIDA Y OBRAS®
ARQUITECTURA