
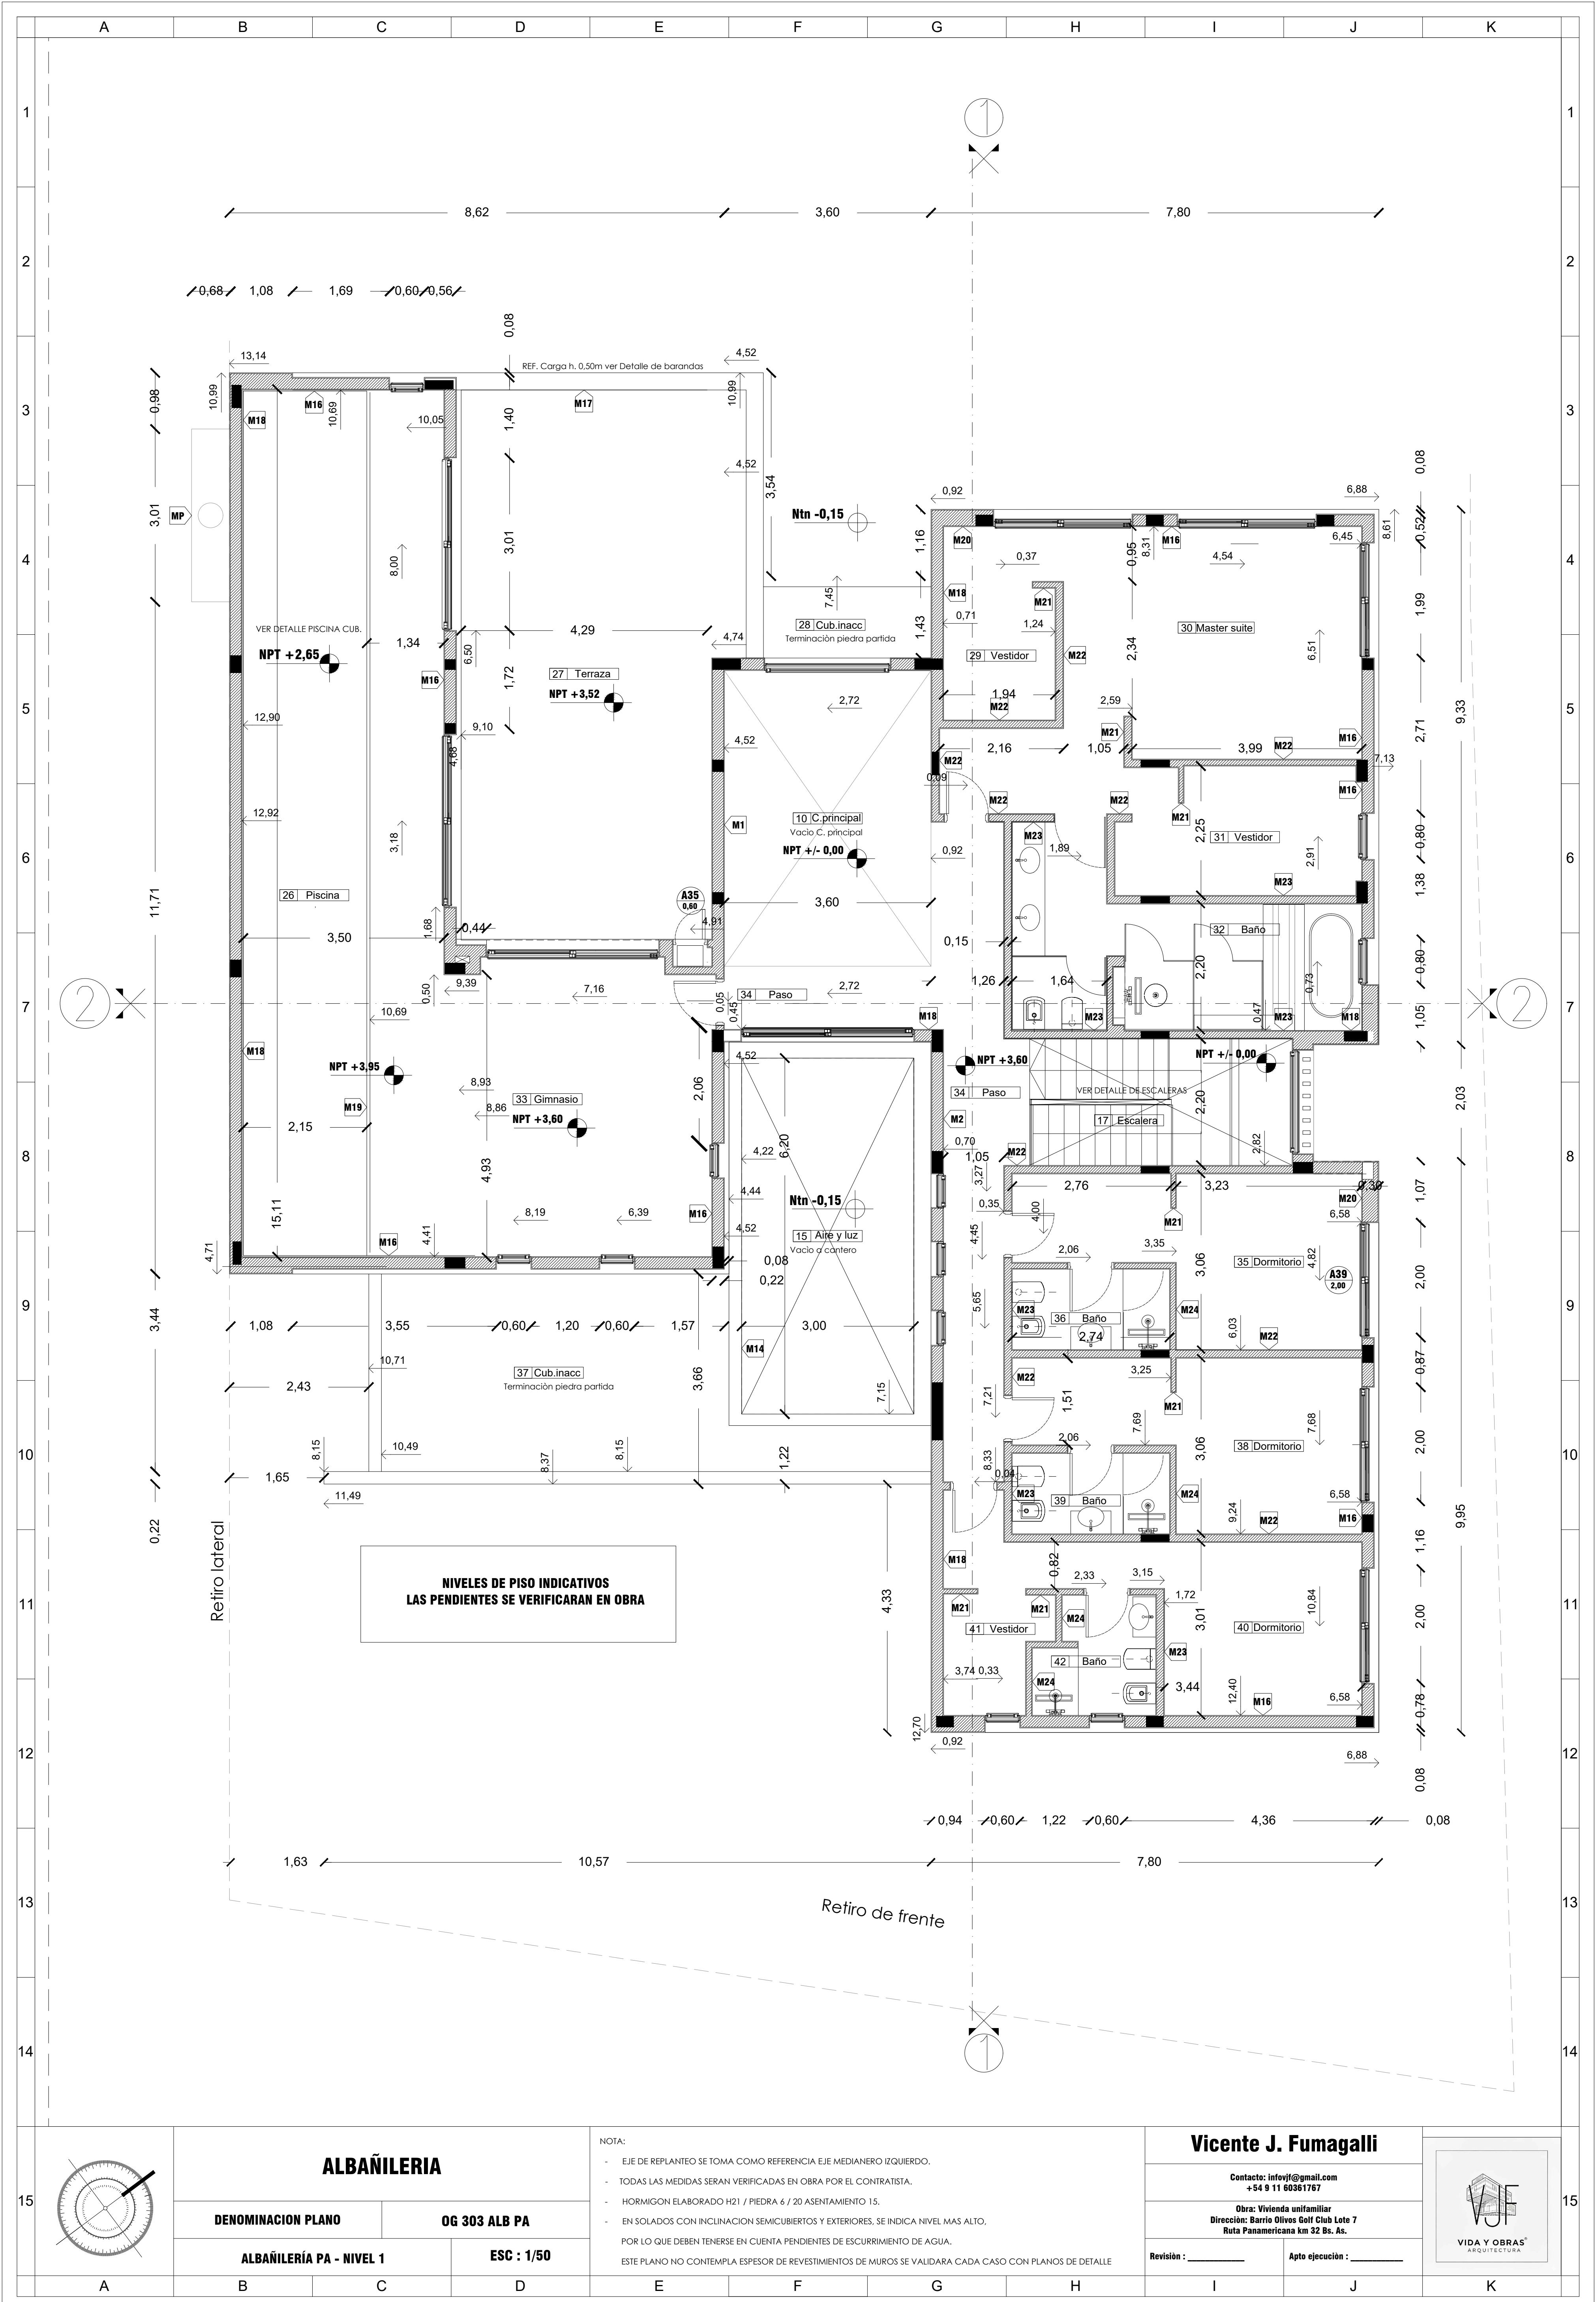


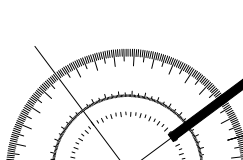

15					ALBAÑILERIA				NOTA: - EJE DE REPLANTEO SE TOMA COMO REFERENCIA EJE MEDIANERO IZQUIERDO. - TODAS LAS MEDIDAS SERÁN VERIFICADAS EN OBRA POR EL CONTRATISTA. - HORMIGON ELABORADO H21 / PIEDRA 6 / 20 ASENTAMIENTO 15. - EN SOLADOS CON INCLINACION SEMICUBIERTOS Y EXTERIORES, SE INDICA NIVEL MAS ALTO, POR LO QUE DEBEN TENERSE EN CUENTA PENDIENTES DE ESCURRIMIENTO DE AGUA. ESTE PLANO NO CONTEMPLA ESPESOR DE REVESTIMIENTOS DE MUROS SE VALIDARA CADA CASO CON PLANOS DE DETALLE				Vicente J. Fumagalli								15																						
	DENOMINACION PLANO				OG 303 ALB PA								Contacto: infovjf@gmail.com +54 9 11 60361767																														
	ALBAÑILERÍA PA - NIVEL 1				ESC : 1/50				Obra: Vivienda unifamiliar Direccion: Barrio Olivos Golf Club Lote 7 Ruta Panamericana km 32 Bs. As.				Revisión : _____				Apto ejecución : _____																										
	A				B				C				D				E					F				G				H				I				J				K	