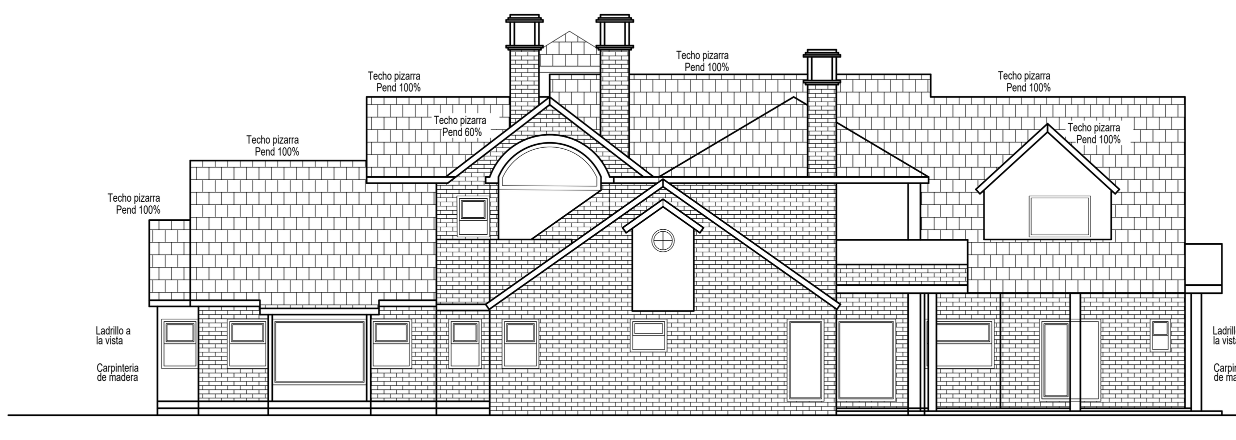

Fachada Calle La Place

ESCALA: 1:100

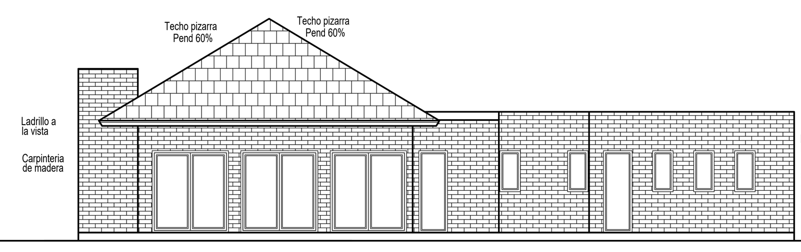

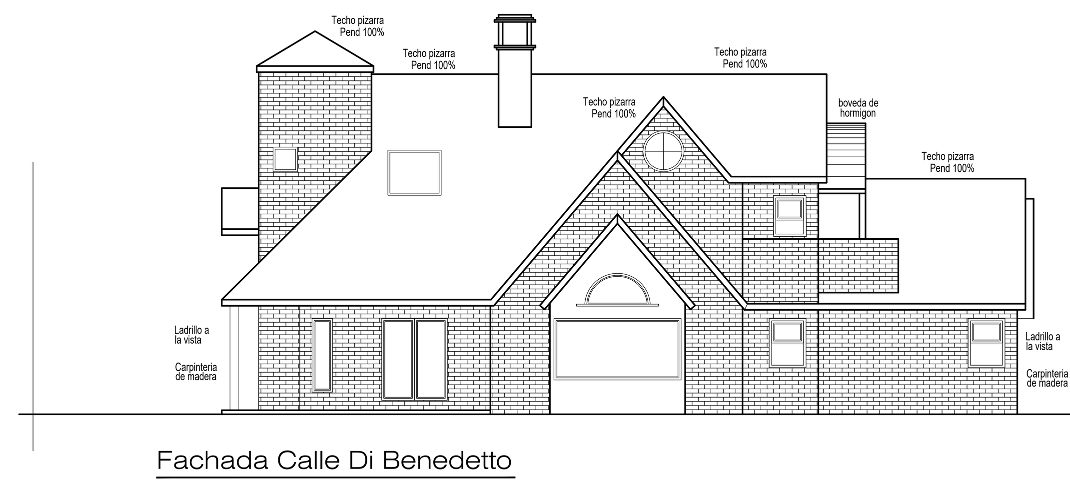

Fachada Calle Di Benedetto

ESCALA: 1:100

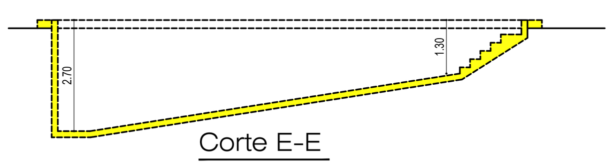

Corte E-E

ESCALA: 1:100

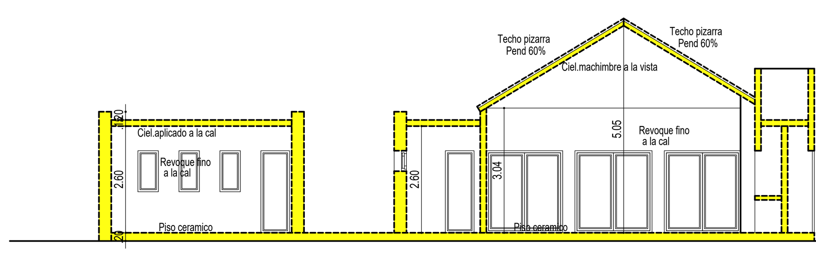

Corte C-C

ESCALA: 1:100

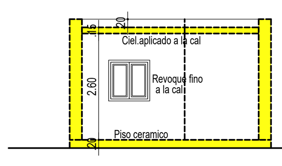

Corte D-D

ESCALA: 1:100

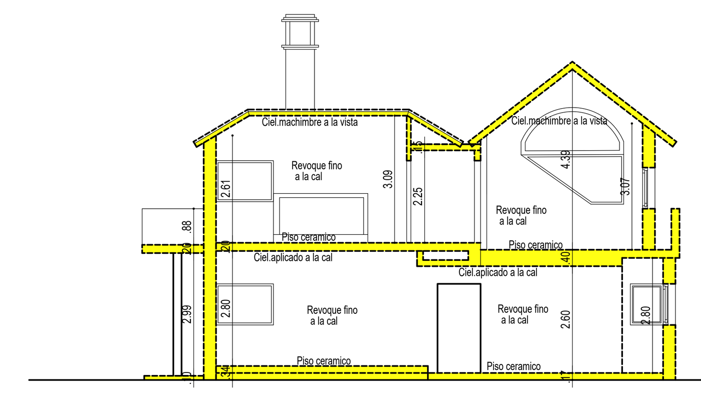

Corte A-A

ESCALA: 1:100

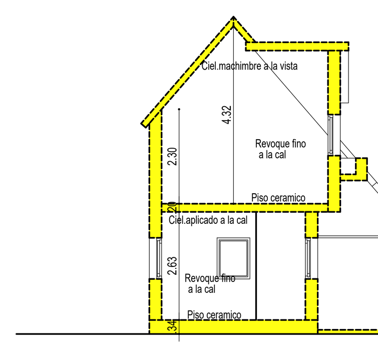

Corte A-A

ESCALA: 1:100

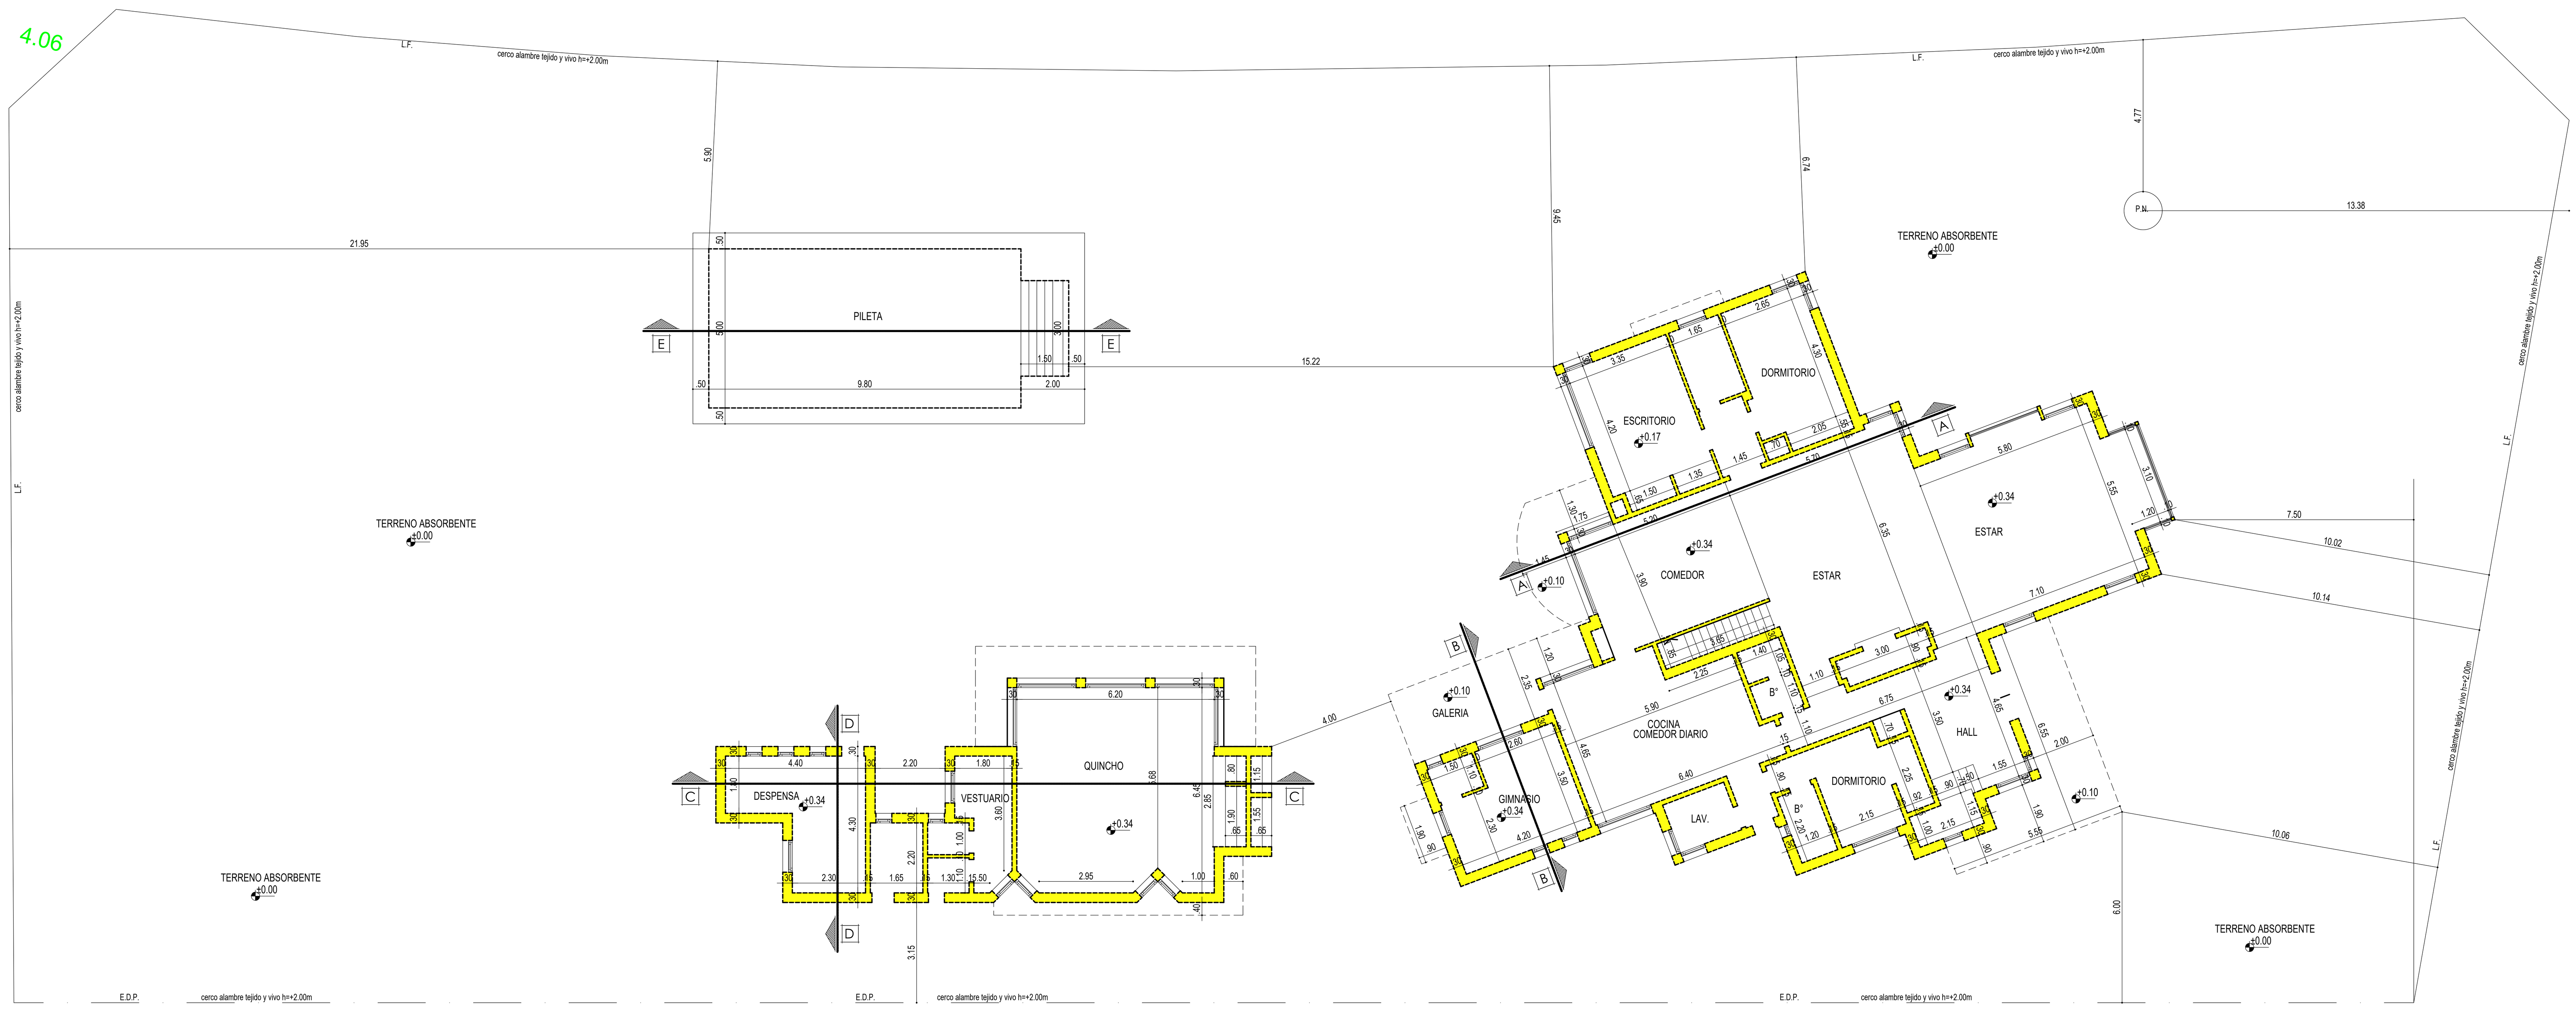

Planta Baja

ESCALA: 1:100

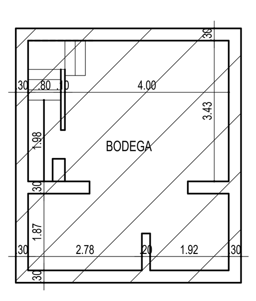

Planta Sotano Vivienda

ESCALA: 1:100

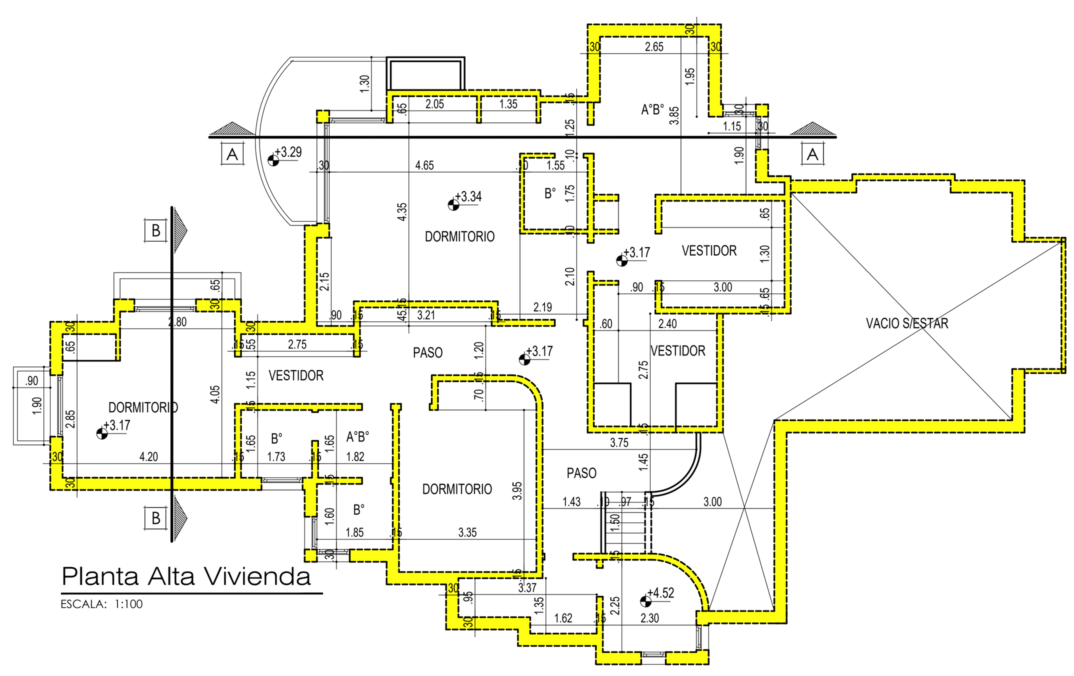

Planta Alta Vivienda

ESCALA: 1:100

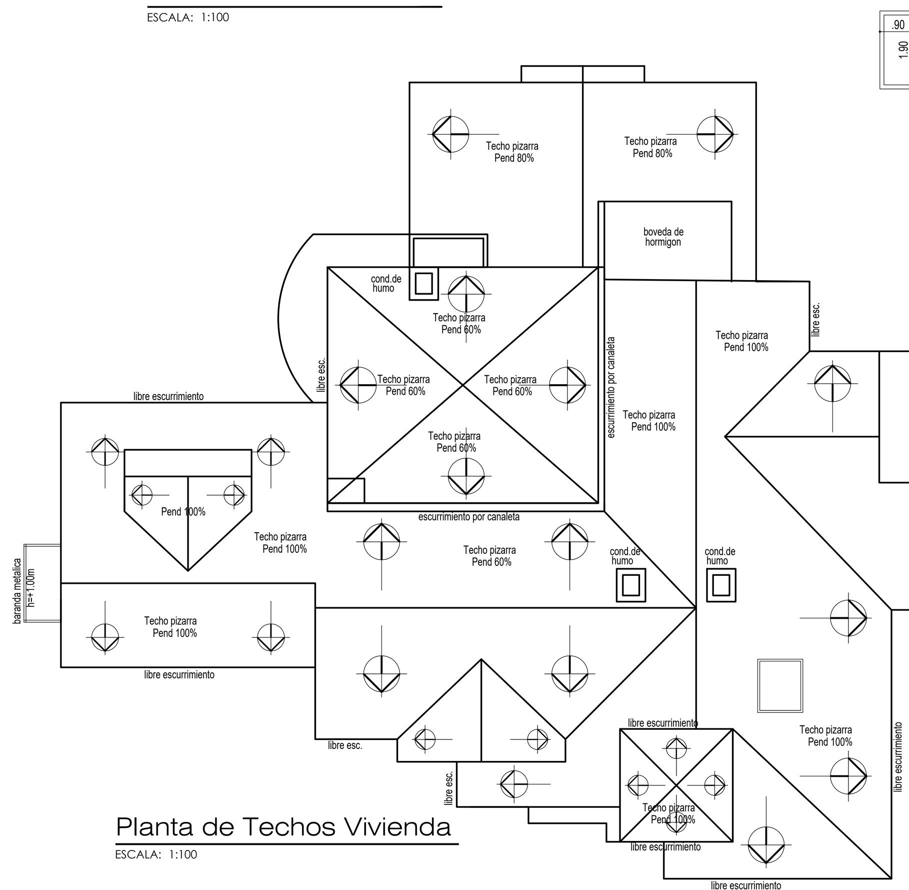

Planta de Techos Vivienda

ESCALA: 1:100

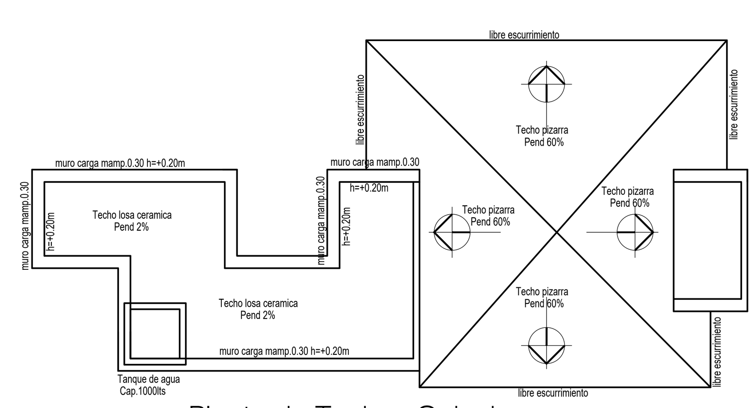

Planta de Techos Quincho

ESCALA: 1:100

estr. de hierro
Pend 5%

CARATULA URBANISTICA
ORDENAMIENTO TERRITORIAL Y USO DEL SUELO

ETAPA DE PROCESO DE ORDENAMIENTO	APROBADAS POR		
	INSTRUMENTO LEGAL	NUMERO	VIGENTE A PARTIR
ZONIFICACION PREVENTIVA	ORDENANZA	00/00	00/00
	ORDENANZA MODIF.	00/00	00/00

UBICACION AREA: ZONA

	SERVICIOS ESENCIALES				
	AGUA CORRIENTE	CLOACAS	GAS	PAVIMENTO	LUZ ELECTRICA
PREVISTO PARA LA ZONA	SI	SI	SI	SI	SI
EXISTENTE EN LA PARCELA					

INDICADORES URBANISTICOS

	D.N. MAX	FOT MAX	FOS MAX	RESTRICCIONES	DIMENSIONES MINIMAS	
ACTUAL	100hab/ha	0.35	0.35		24	1080
POTENCIAL	250hab/ha	0.50	0.50		15	600

USOS PREDOMINANTES: VIVIENDA UNIFAMILIAR
USOS COMPLEMENTARIOS:

FIRMA RESPONSABLE
OFICINA CATASTRO

RETIROS (M)				ALTURA MAXIMA	COCHERA		OBSERVACIONES
	FRENTE	FONDO	LATERALES		CANT	MEDIDAS	
S/C	5.00	10.00	3.00	9.50	1	2.50-5.60	CUMPLE C/ORD 767/04
S/P	5.00	15.00	3.15	7.89	ESP.P/COCH	ESP.P/COCH	Y MODIF. 854/05
CUMPLE	SI	SI	SI	SI			

NORMAS DE USOS Y OCUPACION

PREMIOS	ART. 5.2.4.9.1						
	A	B	C	D	E	F	TOTAL

COMPENSACIONES POR APORTE URBANO	ART. 5.2.4.9.2										
	A	B	C	D	F	G	H	I	J	K	TOTAL

	D.N.MAX	FOS MAX	FOT MAX	INCREMENTO	FOT MAX	D.N. MAX
PARCELA S/C	8	378.00	540.00			
PARCELA S/P	6	317.78	432.65			
CUMPLE	SI	SI	SI			

tachar lo que no corresponde

DECISION FUNDADA DE LA DIRECCION DE ORDENAMIENTO TERRITORIAL

FECHA DE ENTRADA:
FECHA DE SALIDA:
FECHA DE VIGENCIA;

FIRMA RESPONSABLE
OFICINA DE PLANEAMIENTO

PARTIDA MUNICIPAL N° 133-22734

PLANO DE OBRA A DEMOLER

PLANO 1 DE 2

DESTINO: VIVIENDA UNIFAMILIAR Y PILETA

TITULAR DEL PLANO:

HORACIO GROSSO

CALLE: (D-114) DI BENEDETTO N° 4495
S/TITULO: MANZ 17 - LOTE: 1-2
LOCALIDAD: PABLO NOGUES
PARTIDO: MALVINAS ARGENTINAS

ESCALA 1:100
ESCALA 1:200
ESCALA 1:20

UBICACION:

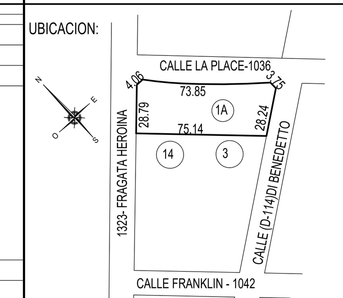

NOMENCLATURA CATASTRAL				ZONIFICACION
CIRC	SECC	MANZ	PARC	
IV	C	17	1A	UE

AREAS		
TERRENO	2335.21m2	
	CUB. m2	S.CUB. m2
A DEMOLER P.B.	351.19	54.06
A DEMOLER P.A.	168.45	0.00
SOTANO APROBADO	34.10	0.00
A DEMOLER PILETA	53.50	
TOTAL A DEMOLER	607.80m2	
LIBRE	2335.21m2	
COEF. DE ABSORCION 30% SUP. MIN. PARC.	2335.21 m²	

LA APROBACION DE LOS PLANOS NO IMPLICA LA HABILITACION DE LA FINCA O LOCALES.

NOTAS:

NOTA 1: DEBERA CUMPLIR CON ORD. 767/04 MODIF. ORD. 854/05 (CUMA) CAP II - ART. 2.1.1.2 Y ARBOLADO EXTERNO E INTERNO.

NOTA 2: LA APROBACION DE LOS PLANOS NO EXIME AL CONSTRUCTOR DE LA RESPONSABILIDAD EMERGENTE DE LA FALTA DE AJUSTES CON LA REGLAMENTACION VIGENTE. LA MUNICIPALIDAD SE LIMITA SOLAMENTE AL VISADO DE LOS CALCULOS DE ESTRUCTURA. EL PROFESIONAL ES EL UNICO RESPONSABLE.

NOTA 3: EL TITULAR SE HACE RESPONSABLE DE ARBITRAR LOS MEDIOS NECESARIOS PARA LA INSTALACION DEUNA CISTERNA Y/O TANQUE RESERVORIO Y/O CUENCA Y CUMPLIR CON LO ESTABLECIDOEN LA ORD N°1839/18.

FIRMAS:

HORACIO GROSSO
Dom.:

MATR - MM:
Dom.:

APROBACION

N°	X	Y	CUB. PB	S/CUB.PB	CUB. PA	S.CUB. PA	SOTANO	PILETA	OBS.
1	8.15	4.85	39.53						A DEMOLER
2	1.40	4.20		5.88					A DEMOLER
3	1.53	1.25		1.91					A DEMOLER
4	3.28	4.15	13.61						A DEMOLER
5	3.65	12.80	46.72						A DEMOLER
6	2.75	12.65	34.79						A DEMOLER
7	1.82	12.65	23.02						A DEMOLER
8	2.50	0.15	0.37						A DEMOLER
9	4.35	2.35		10.22					A DEMOLER
10	2.00	1.20		2.40					A DEMOLER
11	0.35	1.20	0.42						A DEMOLER
12	5.80	6.10	35.38						A DEMOLER
13	1.05	3.30	3.46						A DEMOLER
14	0.90	1.90		1.71					A DEMOLER
15	4.35	4.10	17.83						A DEMOLER
16	2.18	5.25	11.44						A DEMOLER
17	3.45	7.00	24.15						A DEMOLER
18	1.40	0.85		1.19					A DEMOLER
19	2.75	1.00	2.75						A DEMOLER
20	1.83	0.90		1.65					A DEMOLER
21	1.82	1.90		3.46					A DEMOLER
22	1.90	6.60		12.54					A DEMOLER
23	3.10	0.55			1.70				A DEMOLER
24	6.20	4.10			25.42				A DEMOLER
25	0.30	2.35			0.70				A DEMOLER
26	1.45	5.25			7.61				A DEMOLER
27	5.15	5.65			29.10				A DEMOLER
28	3.25	7.05			22.91				A DEMOLER
29	1.15	1.75			2.01				A DEMOLER
30	1.70	3.35			5.69				A DEMOLER
31	3.30	2.85			9.40				A DEMOLER
32	6.90	2.65			18.28				A DEMOLER
33	2.00	3.20			6.40				A DEMOLER
34	1.45	3.75			5.44				A DEMOLER
35	1.75	4.85			8.49				A DEMOLER
36	1.90	5.25			9.97				A DEMOLER
37	1.35	4.40			5.94				A DEMOLER
38	1.20	0.40			0.48				A DEMOLER
39	π x1.20 /2²				2.26				A DEMOLER
40	π x1.40 /2²				3.08				A DEMOLER
41	2.75	1.30			3.57				A DEMOLER
42	5.50	6.20					34.10		APROBADO
43	5.00	2.40	12.00						A DEMOLER
SUBTOTAL			265.47	40.96	168.45	--	34.10	--	

N°	X	Y	CUB. PB	S/CUB.PB	CUB. PA	S.CUB. PA	SOTANO	PILETA	OBS.
SUBTOTAL			265.57	40.96	168.45	--	34.10	--	
44	2.90	2.50	7.25						A DEMOLER
45	2.20	2.80	6.16						A DEMOLER
46	1.95	4.90	9.55						A DEMOLER
47	1.00	2.15		2.15					A DEMOLER
48	8.80	1.00		8.80					A DEMOLER
49	6.80	7.05	57.49						A DEMOLER
50	1.00	2.15		2.15					A DEMOLER
51	1.50	3.45	5.17						A DEMOLER
52	1.50	3.00						4.50	A DEMOLER
53	9.80	5.00						49.00	A DEMOLER
SUBTOTAL			351.19	54.06	168.45	--	34.10	53.50	
SUBTOTAL			607.80						

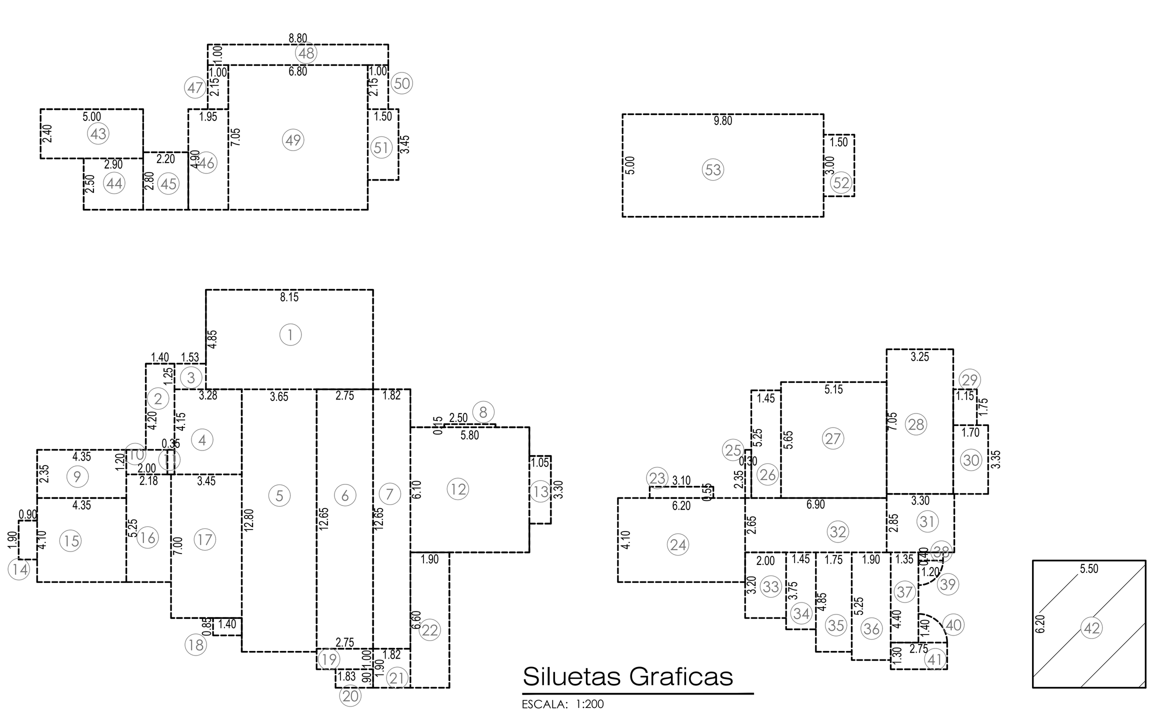

Siluetas Graficas

ESCALA: 1:200

CARATULA URBANISTICA
ORDENAMIENTO TERRITORIAL Y USO DEL SUELO
ETAPA DE PROCESO DE ORDENAMIENTO - APROBADAS POR - INSTRUMENTO LEGAL - NUMERO - VIGENTE A PARTIR
ZONIFICACION PREVENTIVA - ORDENANZA 00/00 00/00 - ORDENANZA MODIF. 00/00 00/00
UBICACION AREA: ZONA
SERVICIOS ESENCIALES: AGUA CORRIENTE SI - CLOACAS SI - GAS SI - PAVIMENTO SI - LUZ ELECTRICA SI
PREVISTO PARA LA ZONA / EXISTENTE EN LA PARCELA
INDICADORES URBANISTICOS
ACTUAL 100hab/ha 0.35 0.35 24 1080
POTENCIAL 250hab/ha 0.50 0.50 15 600
USOS PREDOMINANTES: VIVIENDA UNIFAMILIAR
USOS COMPLEMENTARIOS:
FIRMA RESPONSABLE OFICINA CATASTRO
RETIROS (M) S/C 5.00 10.00 3.00 9.50 1 2.50-5.60 CUMPLE C/ORD 767/04
S/P 5.00 15.00 3.15 7.89 ESP.P/COCH ESP.P/COCH Y MODIF. 854/05
CUMPLE SI SI SI SI
NORMAS DE USOS Y OCUPACION
PREMIOS ART. 5.2.4.9.1
COMPENSACIONES POR APORTE URBANO ART. 5.2.4.9.2
PARCELA S/C 8 378.00 540.00
PARCELA S/P 6 317.78 432.65
CUMPLE SI SI SI
tachar lo que no corresponde
DECISION FUNDADA DE LA DIRECCION DE ORDENAMIENTO TERRITORIAL
FECHA DE ENTRADA:
FECHA DE SALIDA:
FECHA DE VIGENCIA;
FIRMA RESPONSABLE OFICINA DE PLANEAMIENTO
PARTIDA MUNICIPAL N° 133-22734
PLANO DE OBRA A DEMOLER

PLANO 2 DE 2

DESTINO: VIVIENDA UNIFAMILIAR Y PILETA
TITULAR DEL PLANO:
HORACIO GROSSO
CALLE: (D-114) DI BENEDETTO N° 4495
S/TITULO: MANZ 17 - LOTE: 1-2
LOCALIDAD: PABLO NOGUES
PARTIDO: MALVINAS ARGENTINAS
ESCALA 1:100
ESCALA 1:200
ESCALA 1:20
UBICACION:

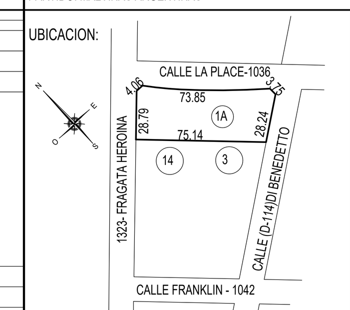

NOMENCLATURA CATASTRAL				ZONIFICACION
CIRC	SECC	MANZ	PARC	
IV	C	17	1-2	UE

AREAS
TERRENO 2335.21m2
A DEMOLER P.B. 351.19 54.06
A DEMOLER P.A. 168.45 0.00
SOTANO APROBADO 34.10 0.00
A DEMOLER PILETA 53.50
TOTAL A DEMOLER 607.80m2
LIBRE 2335.21m2
COEF. DE ABSORCION 30% SUP. MIN. PARC. 2335.21 m²
LA APROBACION DE LOS PLANOS NO IMPLICA LA HABILITACION DE LA FINCA O LOCALES.
NOTAS:
NOTA 1: DEBERA CUMPLIR CON ORD. 767/04 MODIF. ORD. 854/05 (CUMA) CAP II - ART. 2.1.1.2 Y ARBOLADO EXTERNO E INTERNO.
NOTA 2: LA APROBACION DE LOS PLANOS NO EXIME AL CONSTRUCTOR DE LA RESPONSABILIDAD EMERGENTE DE LA FALTA DE AJUSTES CON LA REGLAMENTACION VIGENTE. LA MUNICIPALIDAD SE LIMITA SOLAMENTE AL VISADO DE LOS CALCULOS DE ESTRUCTURA. EL PROFESIONAL ES EL UNICO RESPONSABLE.
NOTA 3: EL TITULAR SE HACE RESPONSABLE DE ARBITRAR LOS MEDIOS NECESARIOS PARA LA INSTALACION DEUNA CISTERNA Y/O TANQUE RESERVORIO Y/O CUENCA Y CUMPLIR CON LO ESTABLECIDOEN LA ORD N°1839/18.
FIRMAS:
HORACIO GROSSO
Dom.:
MATR - MM:
Dom.:
APROBACION