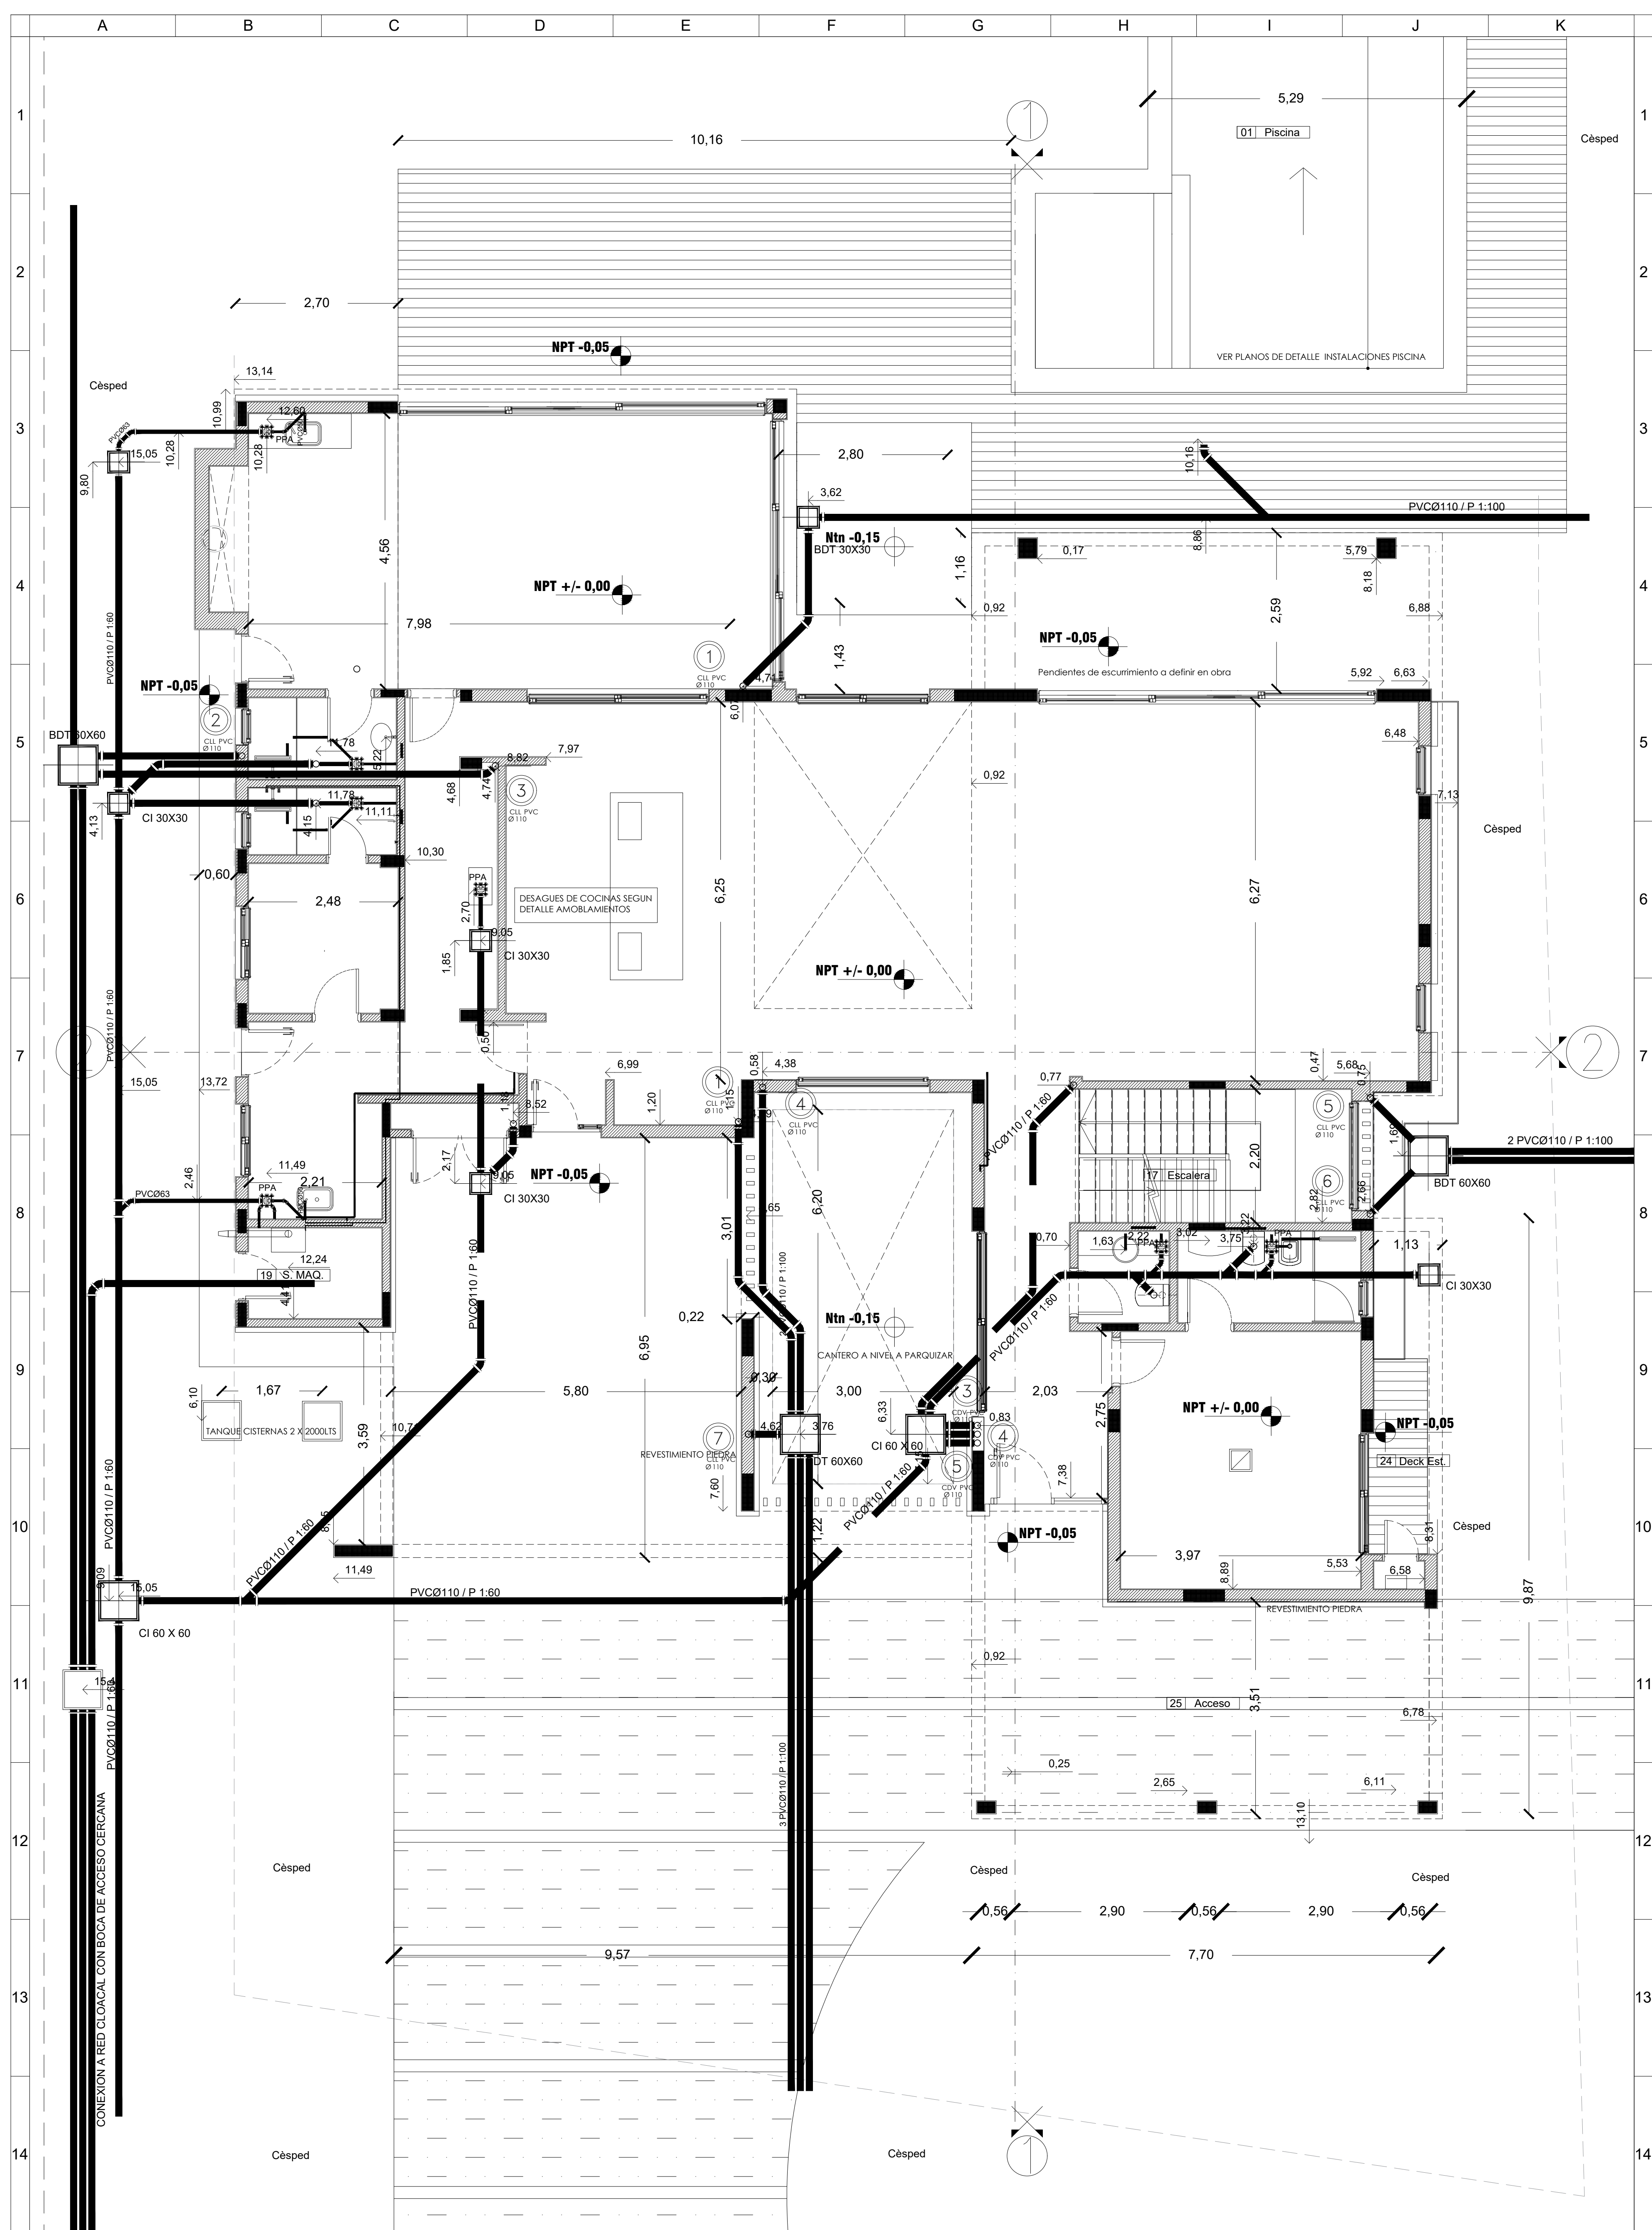


INSTALACION SANITARIA

DENOMINACION PLANO

OG 502 IS DES PL/CL PB

INST. DESAGUES PLUVIALES / CLOACALES PB

ESC : 1/50

NOTA:

- EJE DE REPLANTEO SE TOMA COMO REFERENCIA EJE MEDIANERO IZQUIERDO.
 - TODAS LAS MEDIDAS SERAN VERIFICADAS EN OBRA POR EL CONTRATISTA.
 - PLANO DE REFERENCIA INSTALACION SANITARIA
 - EN SOLADOS CON INCLINACION SEMICUBIERTOS Y EXTERIORES, SE INDICA NIVEL MAS ALTO.
- POR LO QUE DEBEN TENERSE EN CUENTA PENDIENTES DE ESCURRIENTO DE AGUA.

ESTE PLANO NO CONTEMPLA ESPESOR DE REVESTIMIENTOS DE MUROS SE VALIDARA CADA CASO CON PLANOS DE DETALLE

Vicente J. Fumagalli

Contacto: infovjf@gmail.com
+ 51 9 11 99991797

Obra: Vivienda unifamiliar
Dirección: Barrio Olivos Golf Club Lote 7
Ruta Panamericana km 32 Bs. As.

Revision : 10 26

Apto ejecución : _____

VIDA Y OBRAS
ARQUITECTURA